

Точки установки датчиков диагностики и мониторинга в земляное полотно

Верхнее строение пути, земляное полотно и откосы железнодорожного пути.
Испытательный полигон Алабушево — Новая Тверь (для проведения комплексных испытаний).

31

точка установки

13

стрелочных переводов

16

подходов к ИССО

1

высокая насыпь

1

глубокая выемка

Точки 1-3

Стрелочные переводы

ст. Новая Тверь, в направлении Логовежи

СХЕМА УЧАСТКА

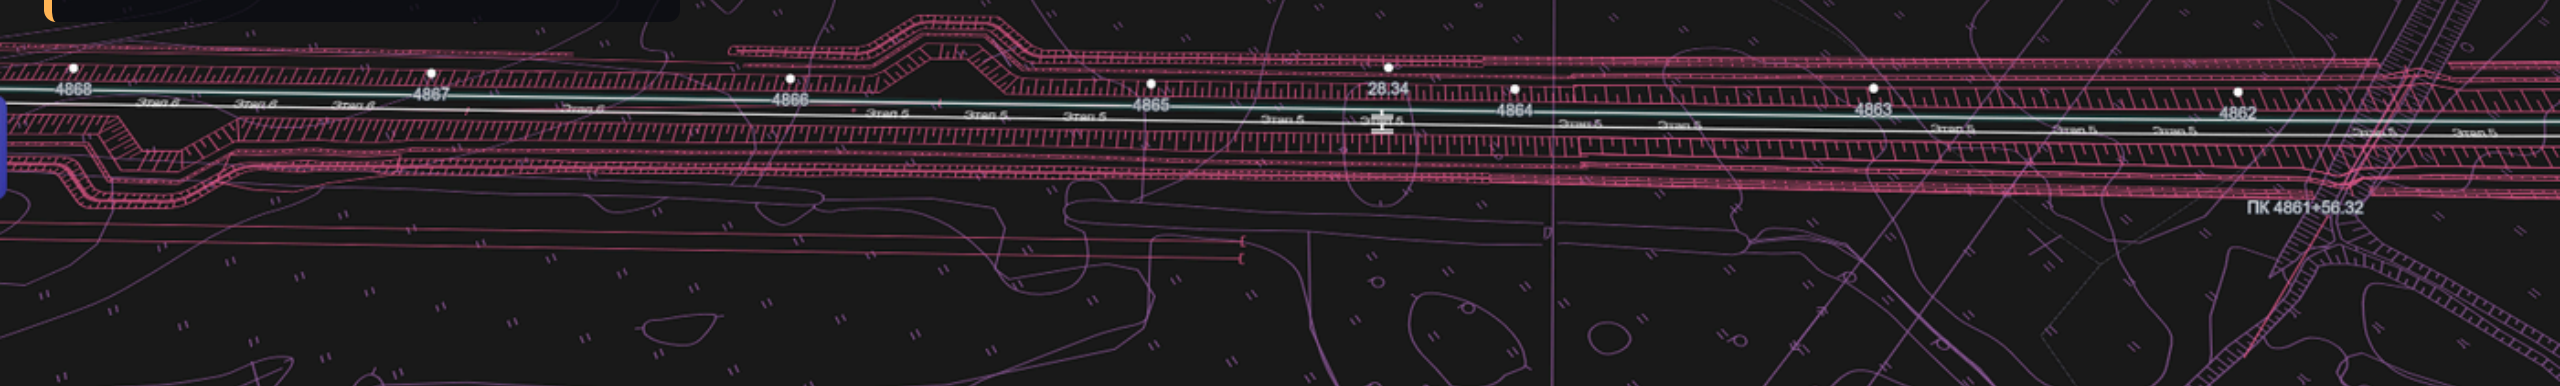


ФОТО С КВАДРОКОПТЕРА

Т. 1 • ПК 4865+49,32

I путь, стрелочный перевод левый нечётный. ПДМ: замена слабого грунта основания на глубину 1 м + забивные сваи 9 м. Поперечный профиль I.

Т. 2 • ПК 4866+77,72

II путь, стрелочный перевод левый чётный. ПДМ: замена слабого грунта основания на глубину 4 м. Поперечный профиль I.

Т. 3 • ПК 4868+26,36

II путь, стрелочный перевод левый нечётный. ПДМ: забивные сваи 19 м. Поперечный профиль III.

Опасные процессы: заболачивание (основание сырое, грунты водонасыщенные), постоянное подтопление, карстовые процессы (категория опасности — опасная).

Точки 4-5

Стрелочные переводы
ст. Новая Тверь, в направлении Логовежи

СХЕМА УЧАСТКА


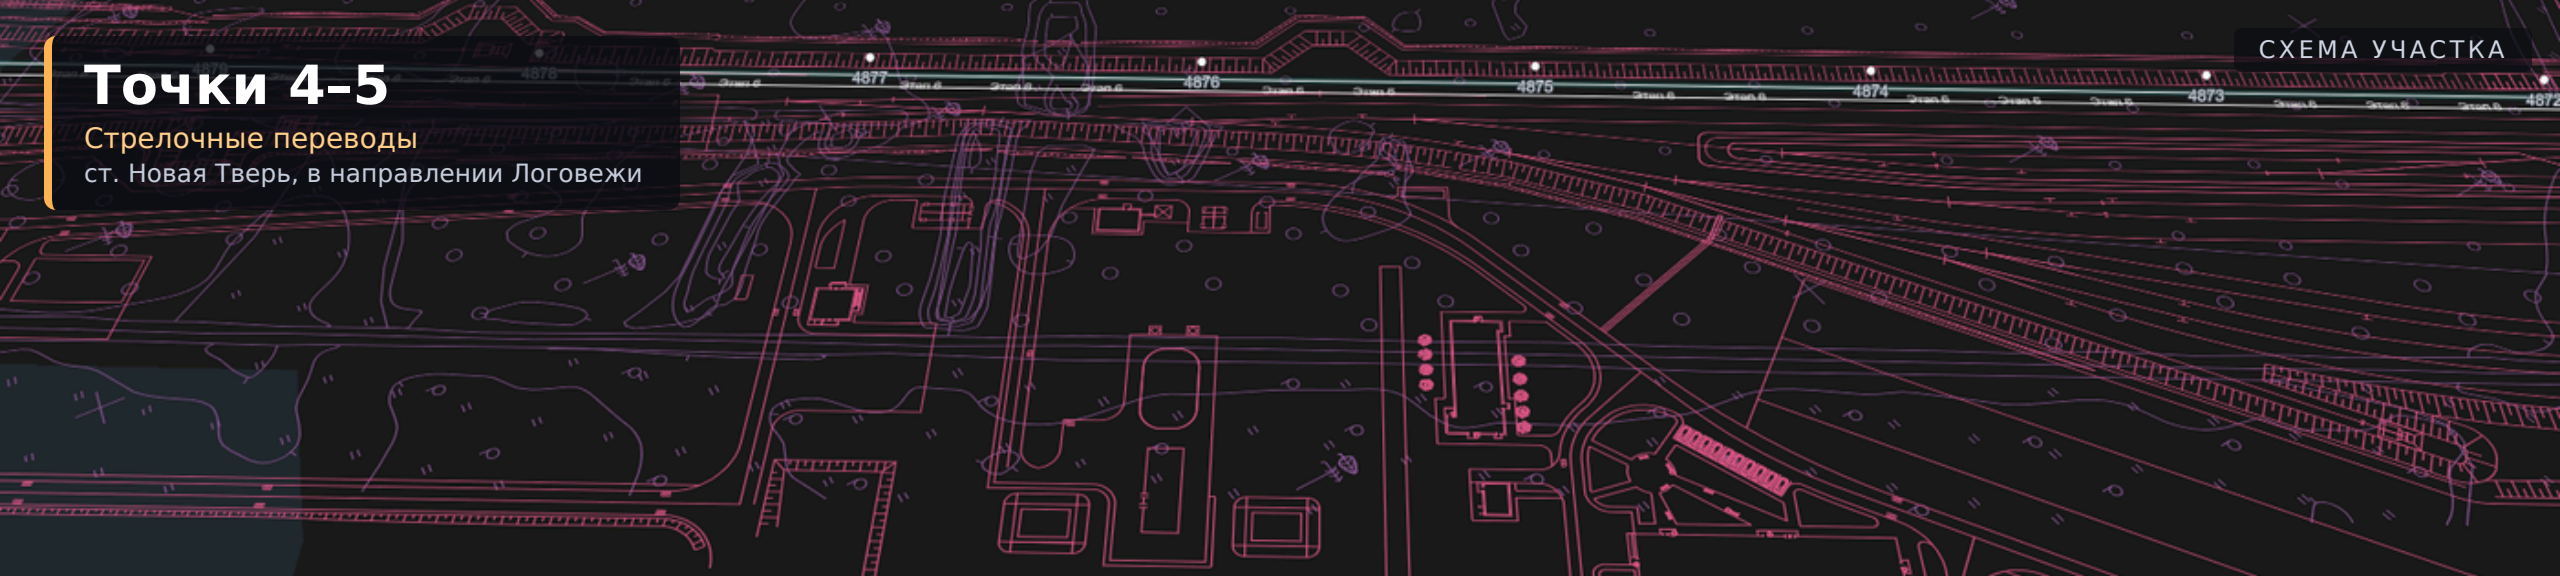


ФОТО С КВАДРОКОПТЕРА

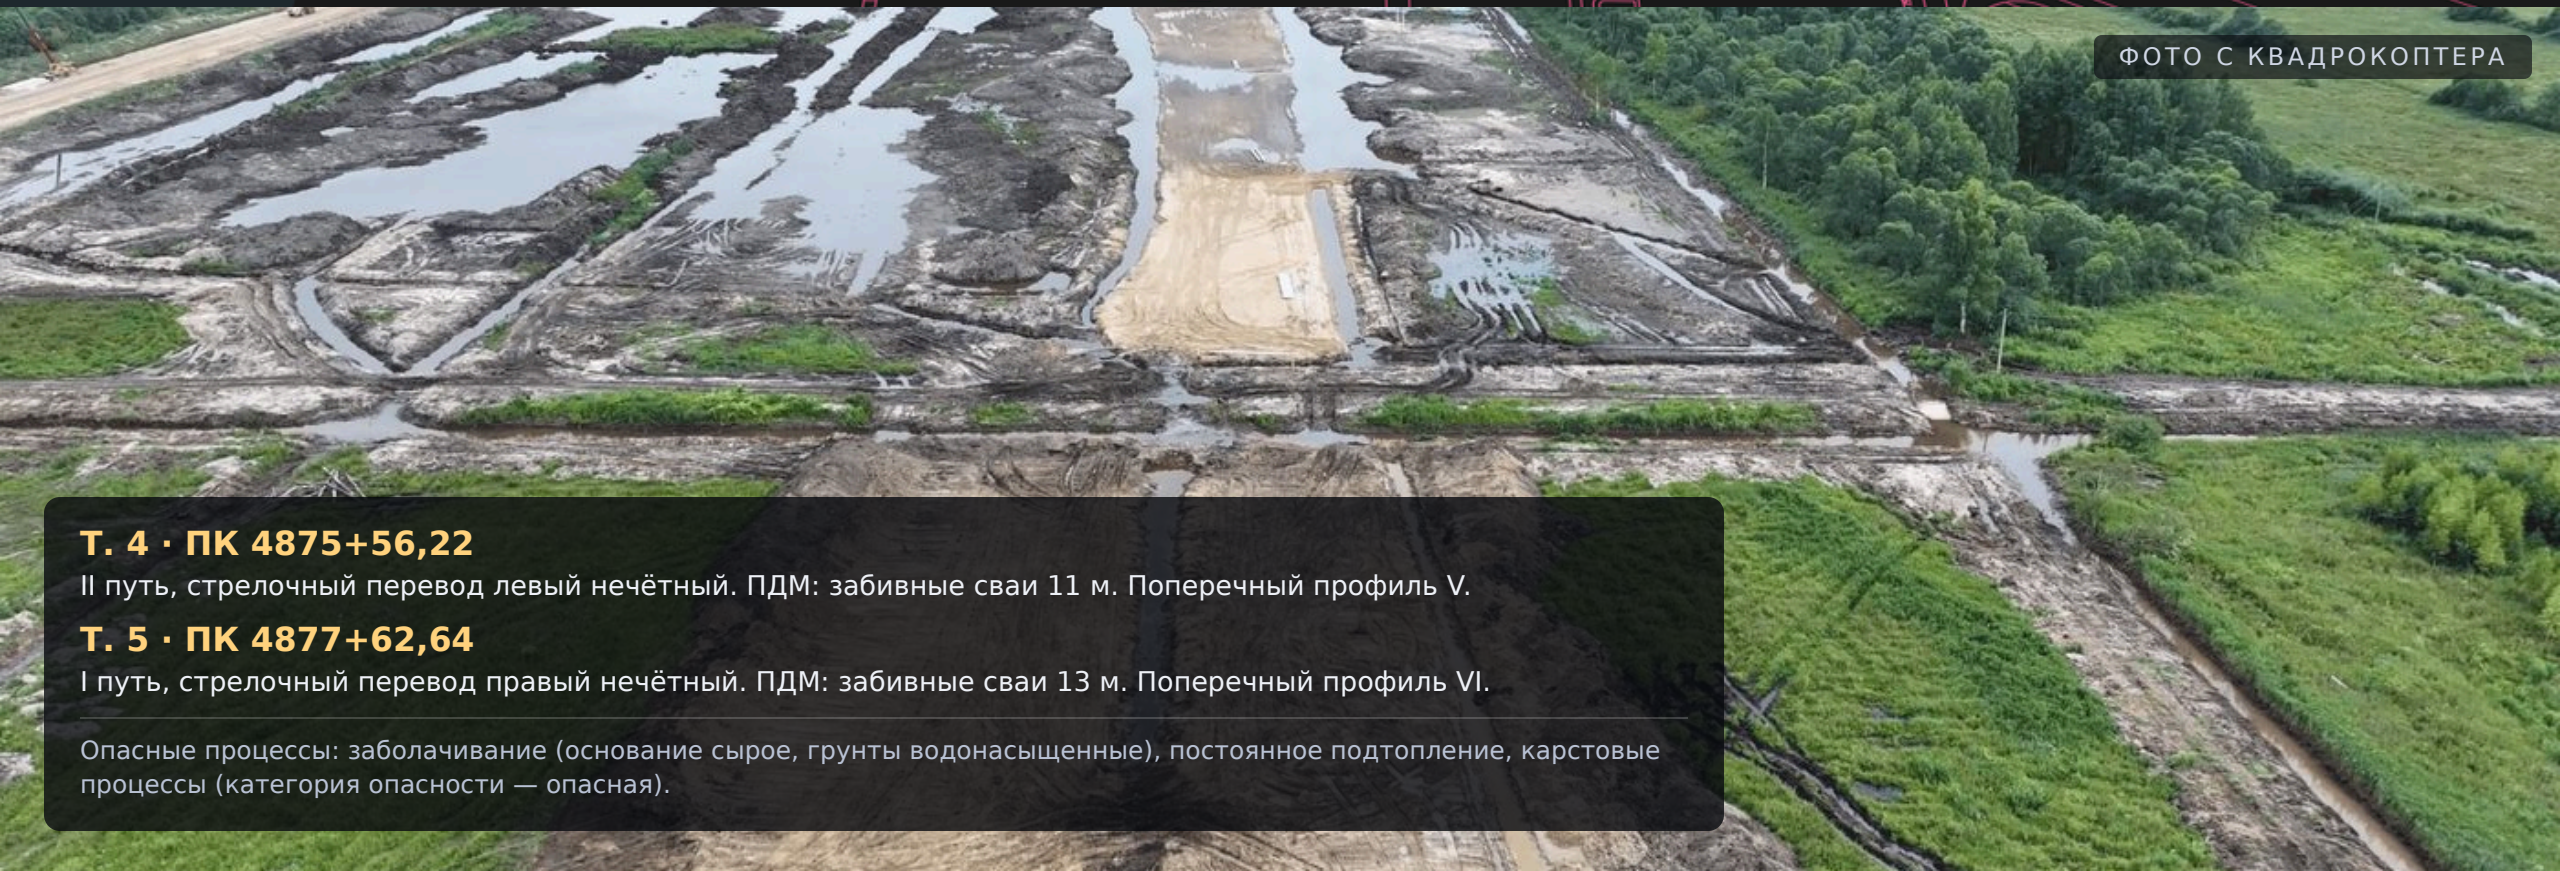

Т. 4 · ПК 4875+56,22

II путь, стрелочный перевод левый нечётный. ПДМ: забивные сваи 11 м. Поперечный профиль V.

Т. 5 · ПК 4877+62,64

I путь, стрелочный перевод правый нечётный. ПДМ: забивные сваи 13 м. Поперечный профиль VI.

Опасные процессы: заболачивание (основание сырое, грунты водонасыщенные), постоянное подтопление, карстовые процессы (категория опасности — опасная).

Точка 6


Стрелочные переводы

ст. Новая Тверь, в направлении Высоково

СХЕМА УЧАСТКА



ФОТО С КВАДРОКОПТЕРА

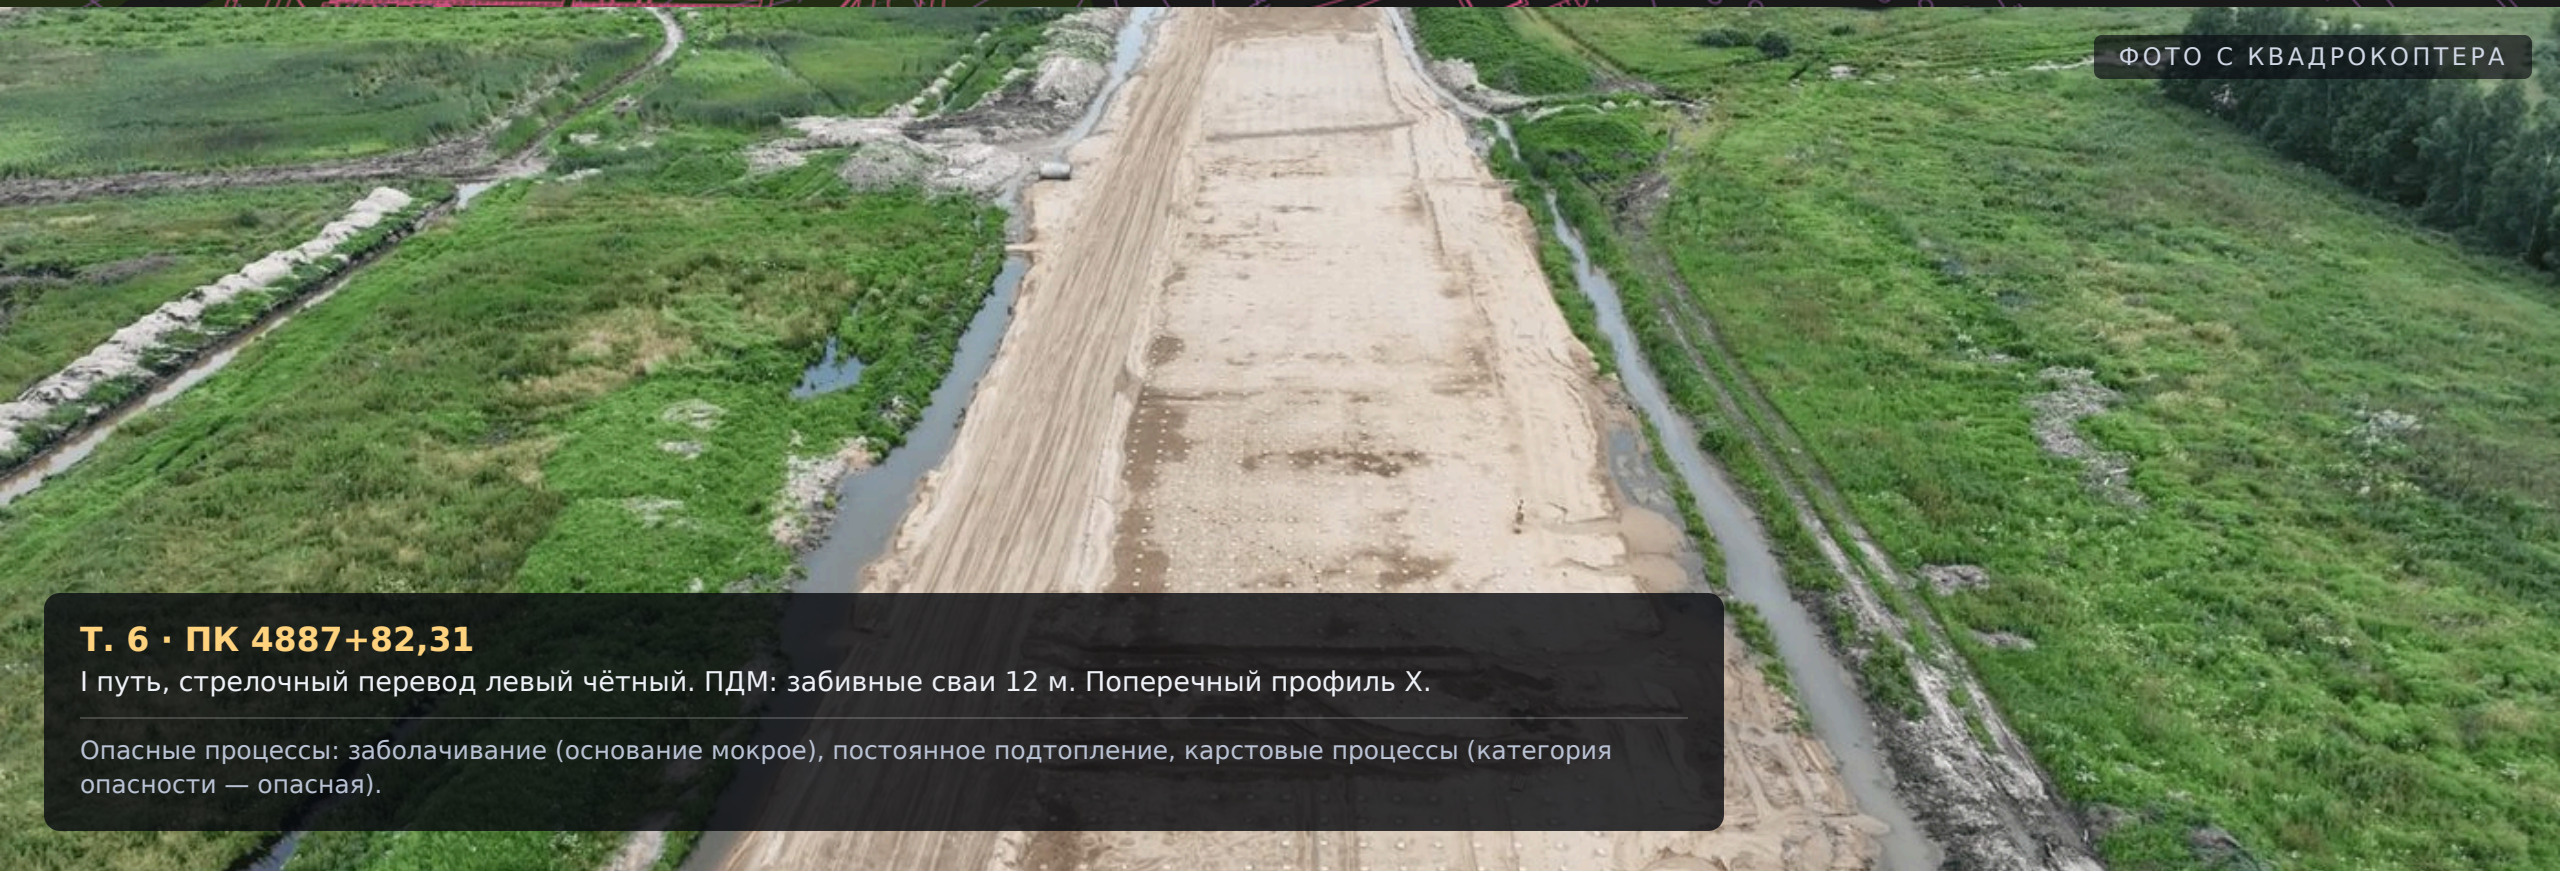

Т. 6 · ПК 4887+82,31

I путь, стрелочный перевод левый чётный. ПДМ: забивные сваи 12 м. Поперечный профиль X.

Опасные процессы: заболачивание (основание мокрое), постоянное подтопление, карстовые процессы (категория опасности — опасная).

Точки 7-9


Стрелочные переводы

ст. Новая Тверь, в направлении Высоково

СХЕМА УЧАСТКА



ФОТО С КВАДРОКОПТЕРА

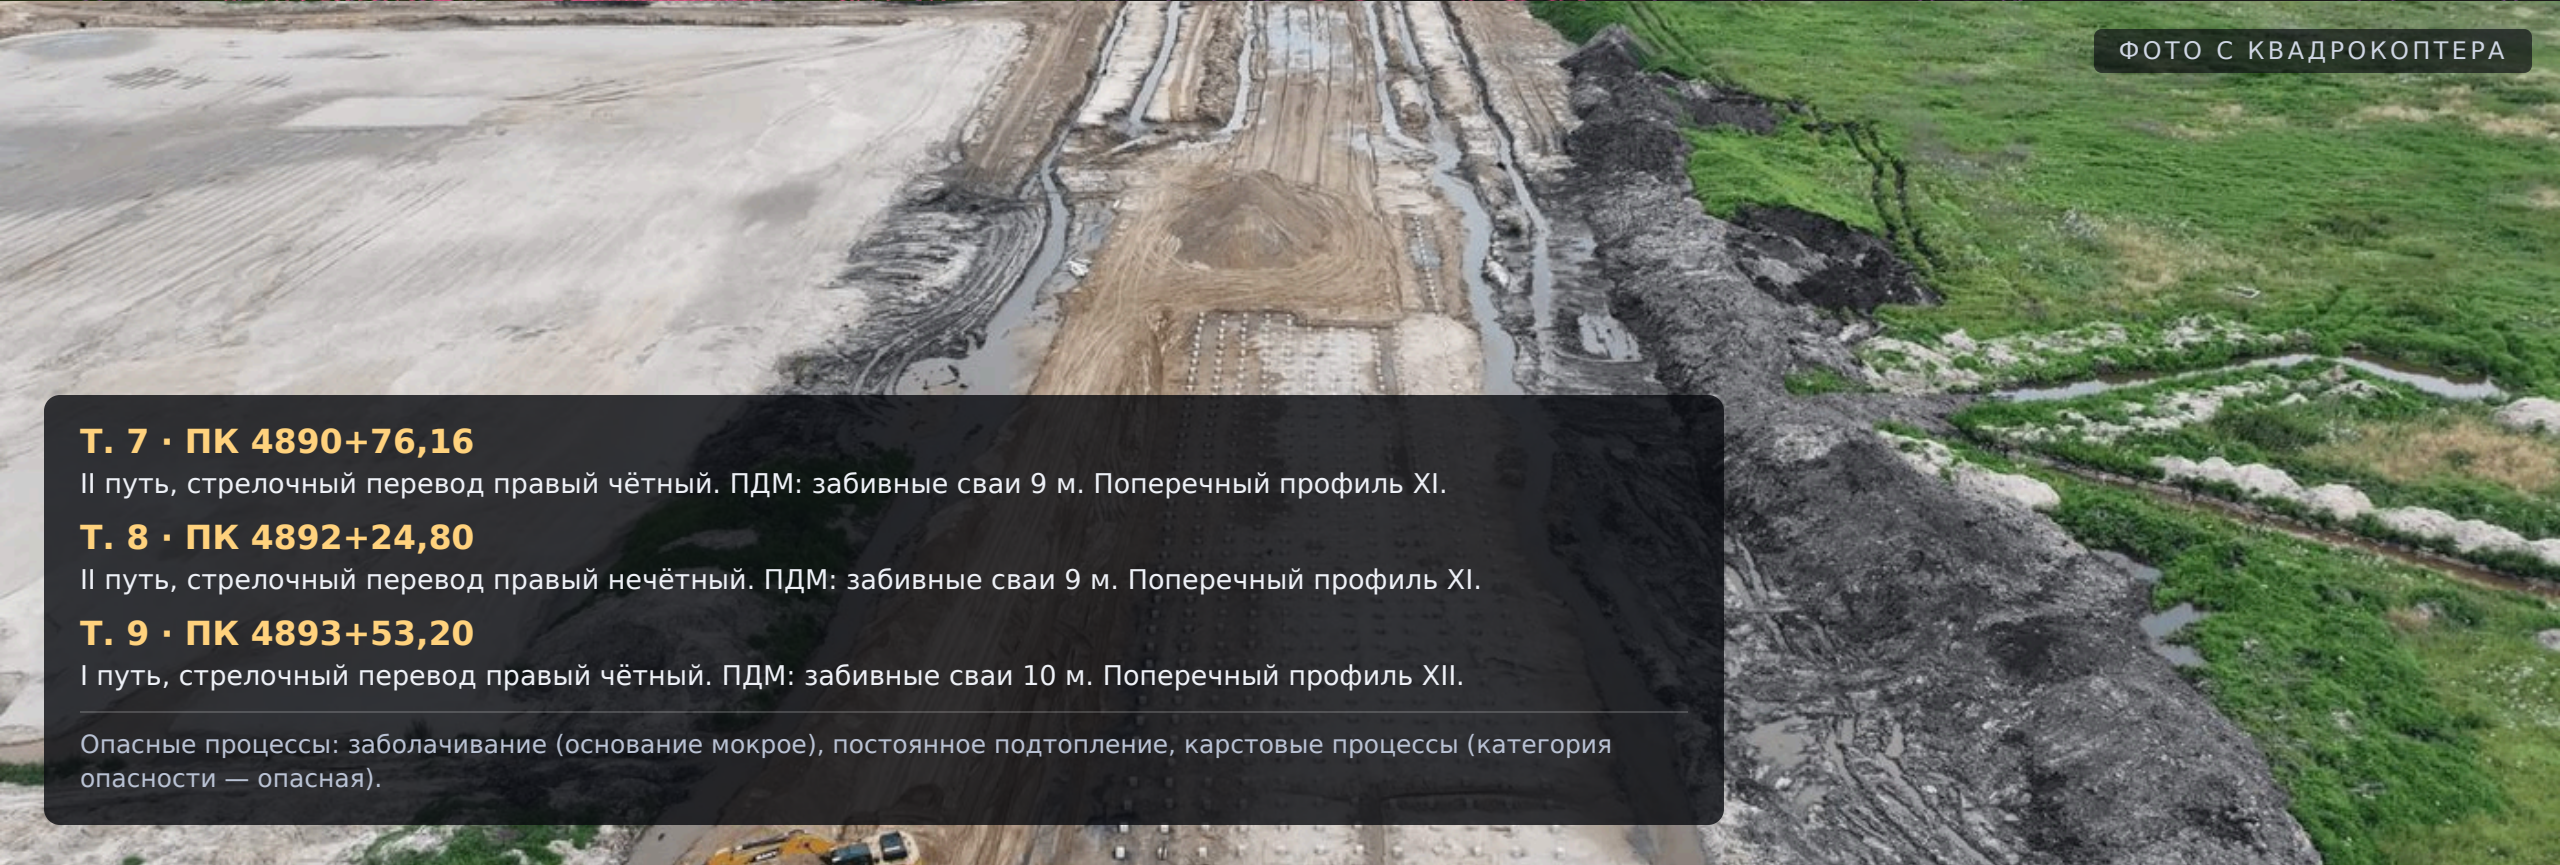

Т. 7 · ПК 4890+76,16

II путь, стрелочный перевод правый чётный. ПДМ: забивные сваи 9 м. Поперечный профиль XI.

Т. 8 · ПК 4892+24,80

II путь, стрелочный перевод правый нечётный. ПДМ: забивные сваи 9 м. Поперечный профиль XI.

Т. 9 · ПК 4893+53,20

I путь, стрелочный перевод правый чётный. ПДМ: забивные сваи 10 м. Поперечный профиль XII.

Опасные процессы: заболачивание (основание мокрое), постоянное подтопление, карстовые процессы (категория опасности — опасная).

Точки 10-11

Стрелочные переводы

вблизи диспетчерского поста 535 км (ПК 5151+47,96), в направлении Новой Твери

СХЕМА УЧАСТКА


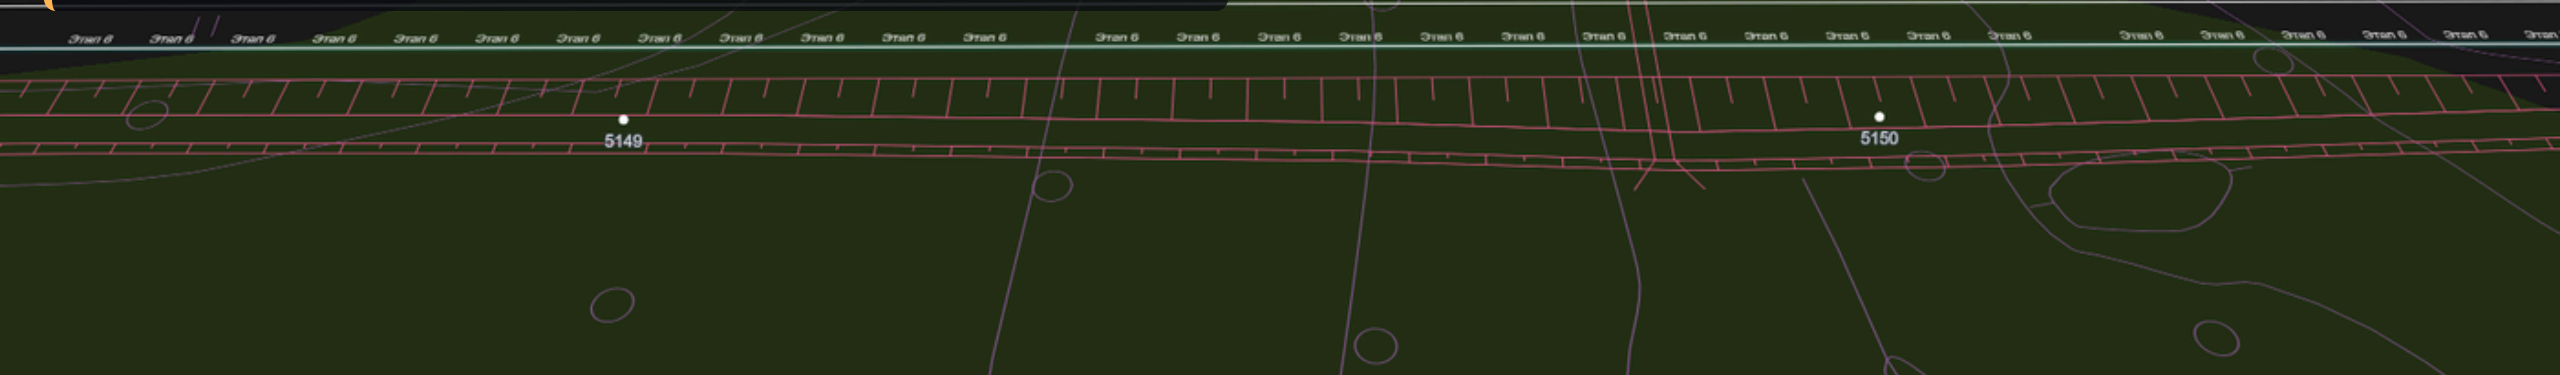


ФОТО С КВАДРОКОПТЕРА

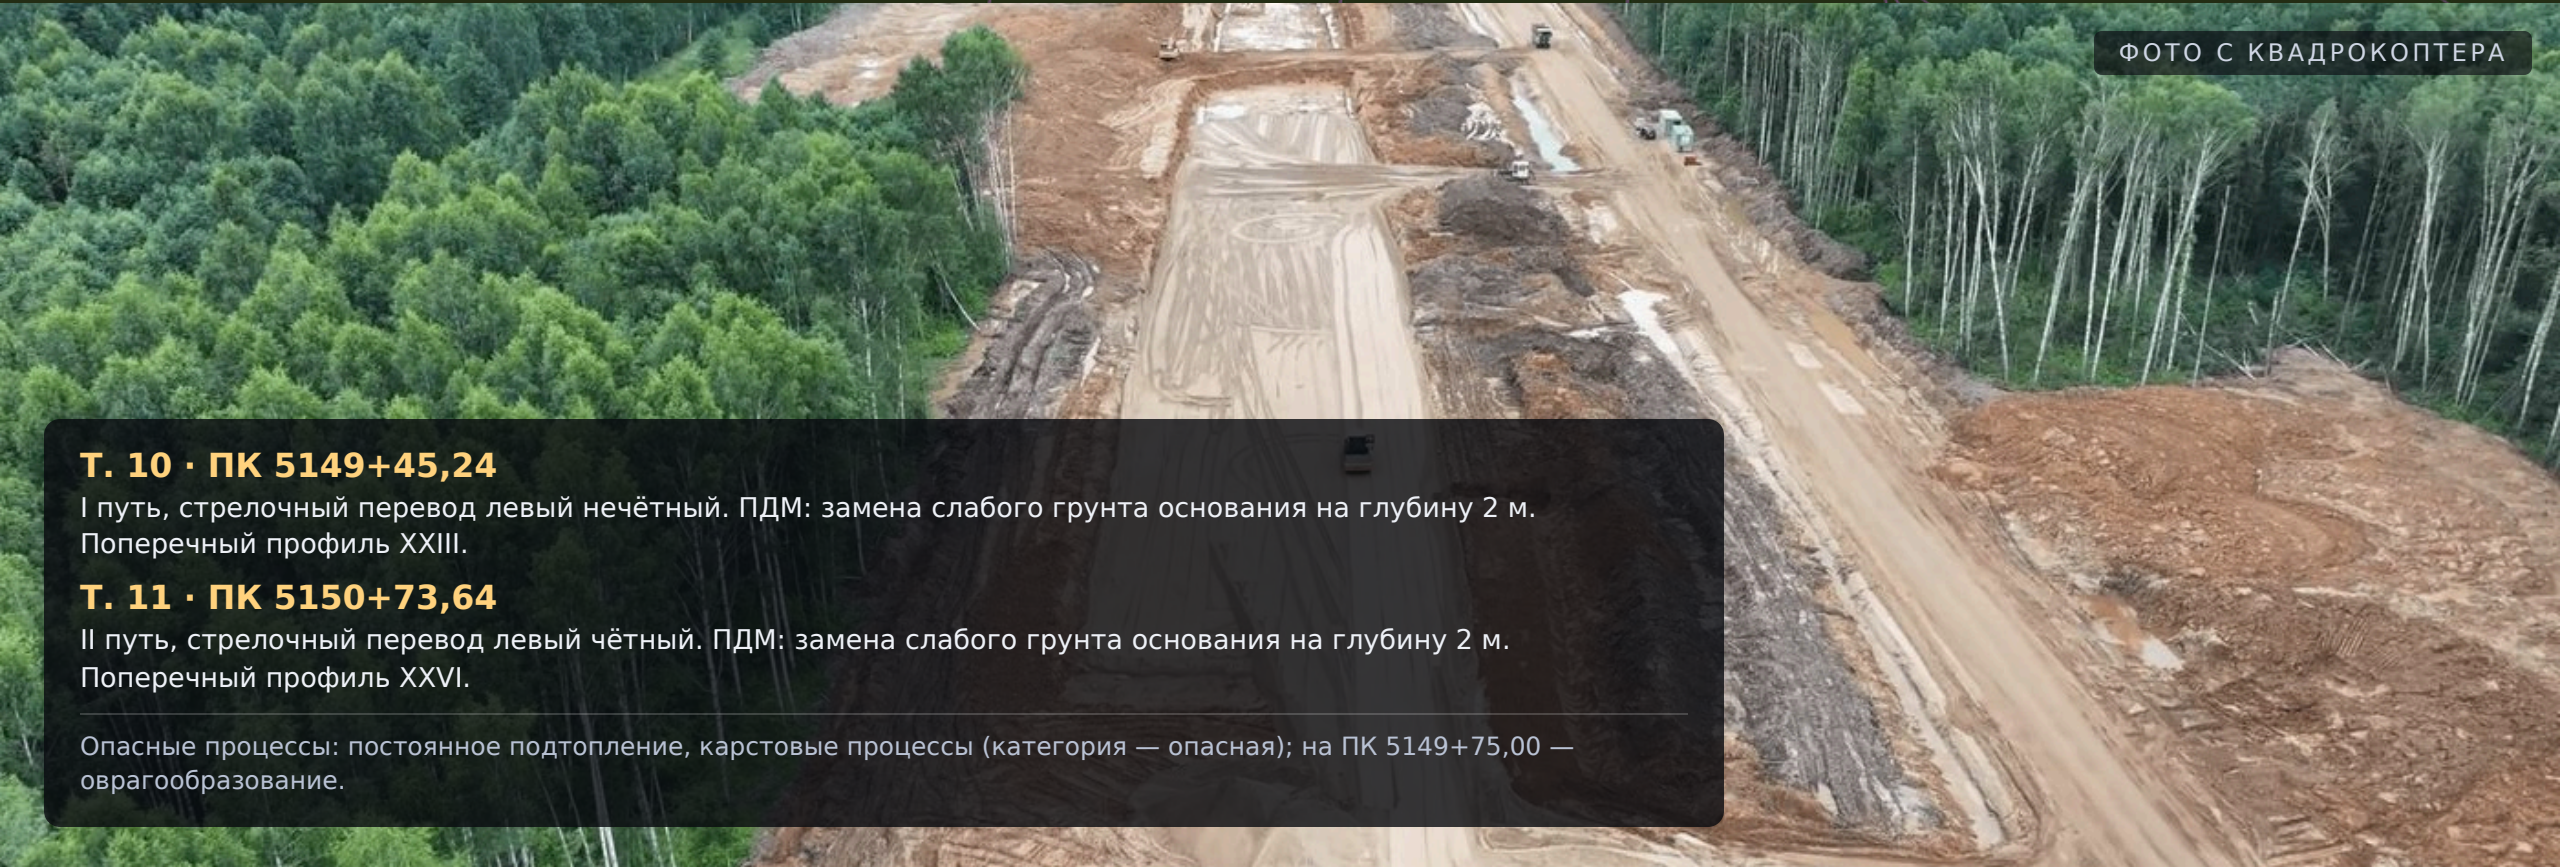

Т. 10 • ПК 5149+45,24

I путь, стрелочный перевод левый нечётный. ПДМ: замена слабого грунта основания на глубину 2 м. Поперечный профиль XXIII.

Т. 11 • ПК 5150+73,64

II путь, стрелочный перевод левый чётный. ПДМ: замена слабого грунта основания на глубину 2 м. Поперечный профиль XXVI.

Опасные процессы: постоянное подтопление, карстовые процессы (категория — опасная); на ПК 5149+75,00 — оврагообразование.

Точки 12-13


Стрелочные переводы

вблизи диспетчерского поста 535 км (ПК 5151+47,96), в направлении Высоково

СХЕМА УЧАСТКА



ФОТО С КВАДРОКОПТЕРА

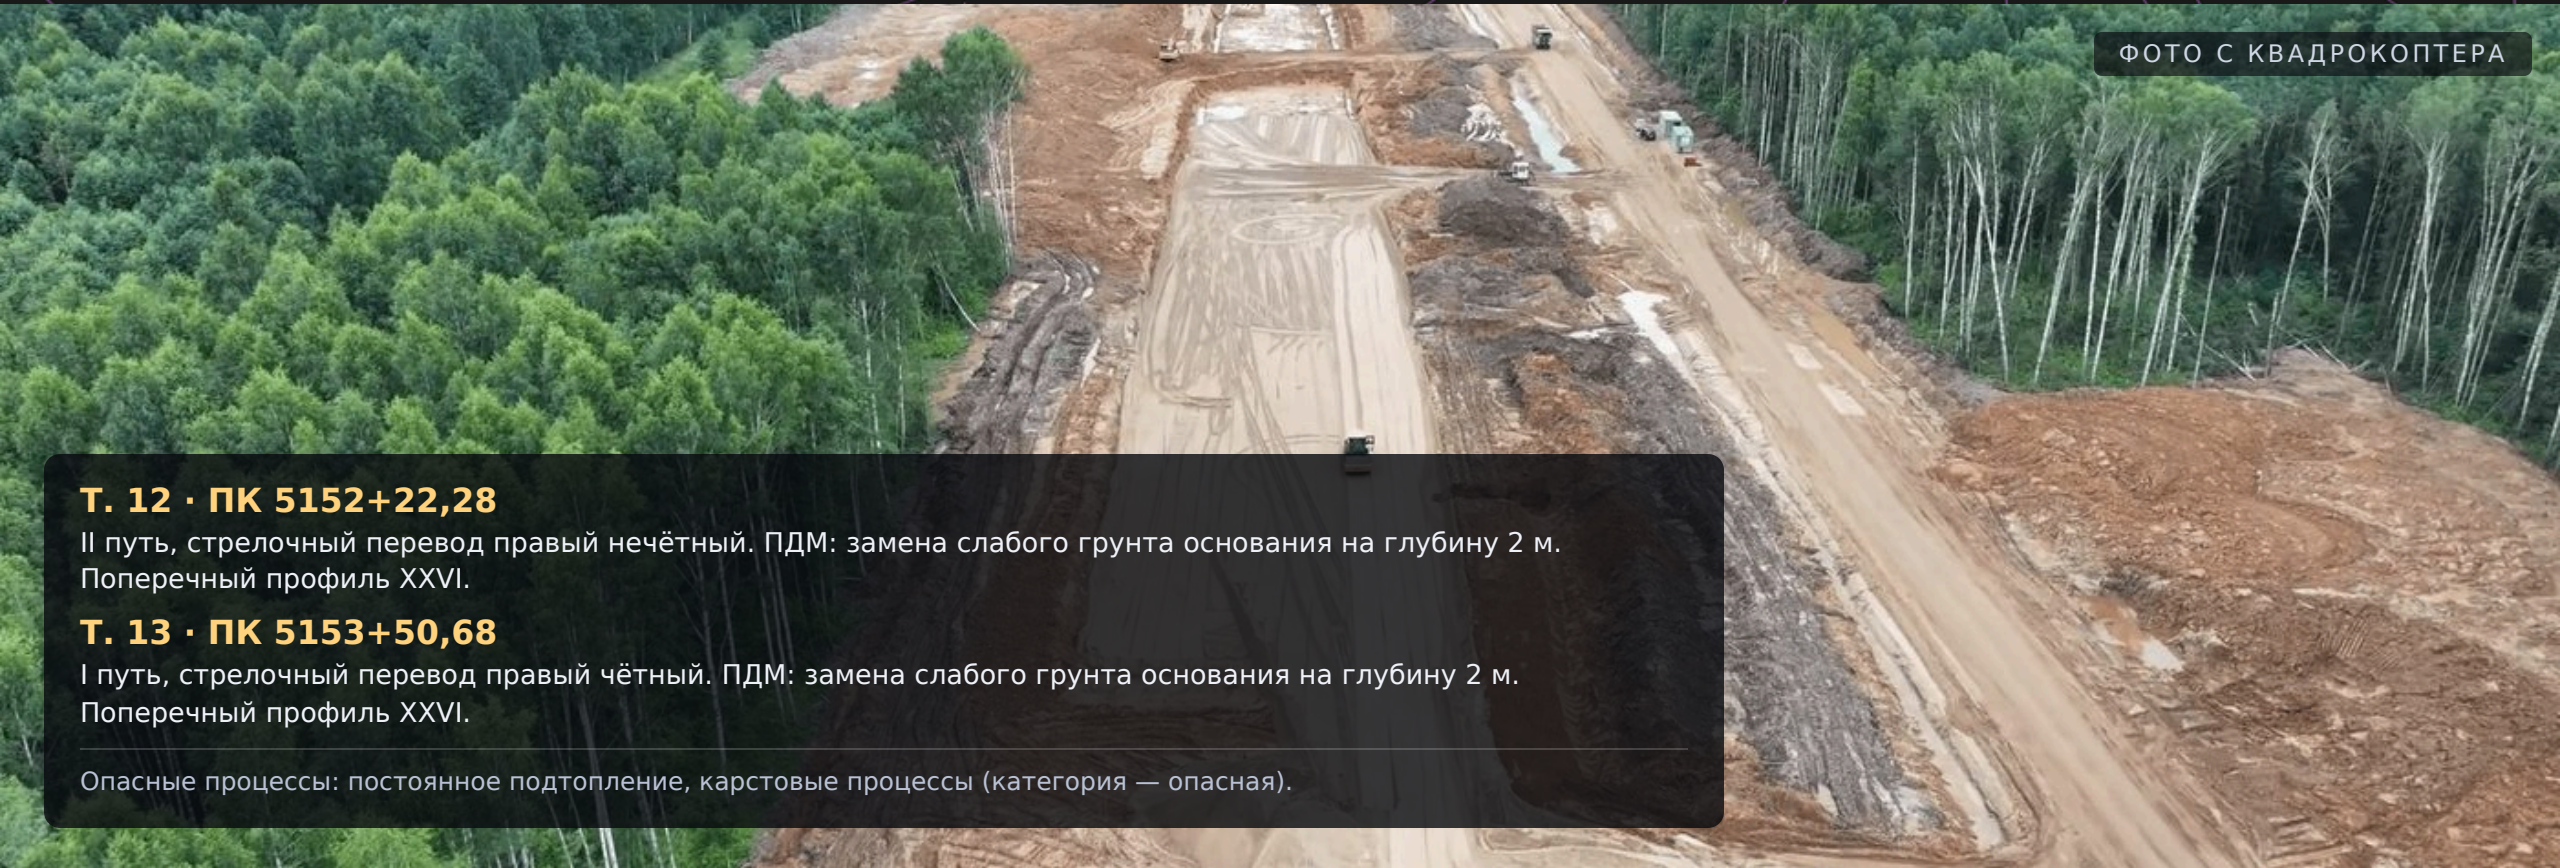

Т. 12 · ПК 5152+22,28

II путь, стрелочный перевод правый нечётный. ПДМ: замена слабого грунта основания на глубину 2 м. Поперечный профиль XXVI.

Т. 13 · ПК 5153+50,68

I путь, стрелочный перевод правый чётный. ПДМ: замена слабого грунта основания на глубину 2 м. Поперечный профиль XXVI.

Опасные процессы: постоянное подтопление, карстовые процессы (категория — опасная).

Точка 14

Подходы к ИССО · ж/д мост (р. Крапивня)
за Новой Тверью, в направлении ДП 535 км (ПК 5151+47,96)

СХЕМА УЧАСТКА

4931

ФОТО С КВАДРОКОПТЕРА

ПК 4931+20,33 - ПК 4938+19,34

Подход на ПК 4931+20,33 — насыпь III типа, УПЖ 25 м, высота насыпи 3,97 м; ПДМ до ПК 4930+90 — забивные сваи 10 м. Подход на ПК 4938+19,34 — насыпь XVIII типа, УПЖ 29,55 м, высота 4,91 м; ПДМ — замена слабого грунта на глубину 2 м + забивные сваи 21 м.

Точка 15

Подходы к ИССО · ж/д мост

за р. Крапивня, в направлении ДП 535 км (ПК 5151+47,96)

СХЕМА УЧАСТКА

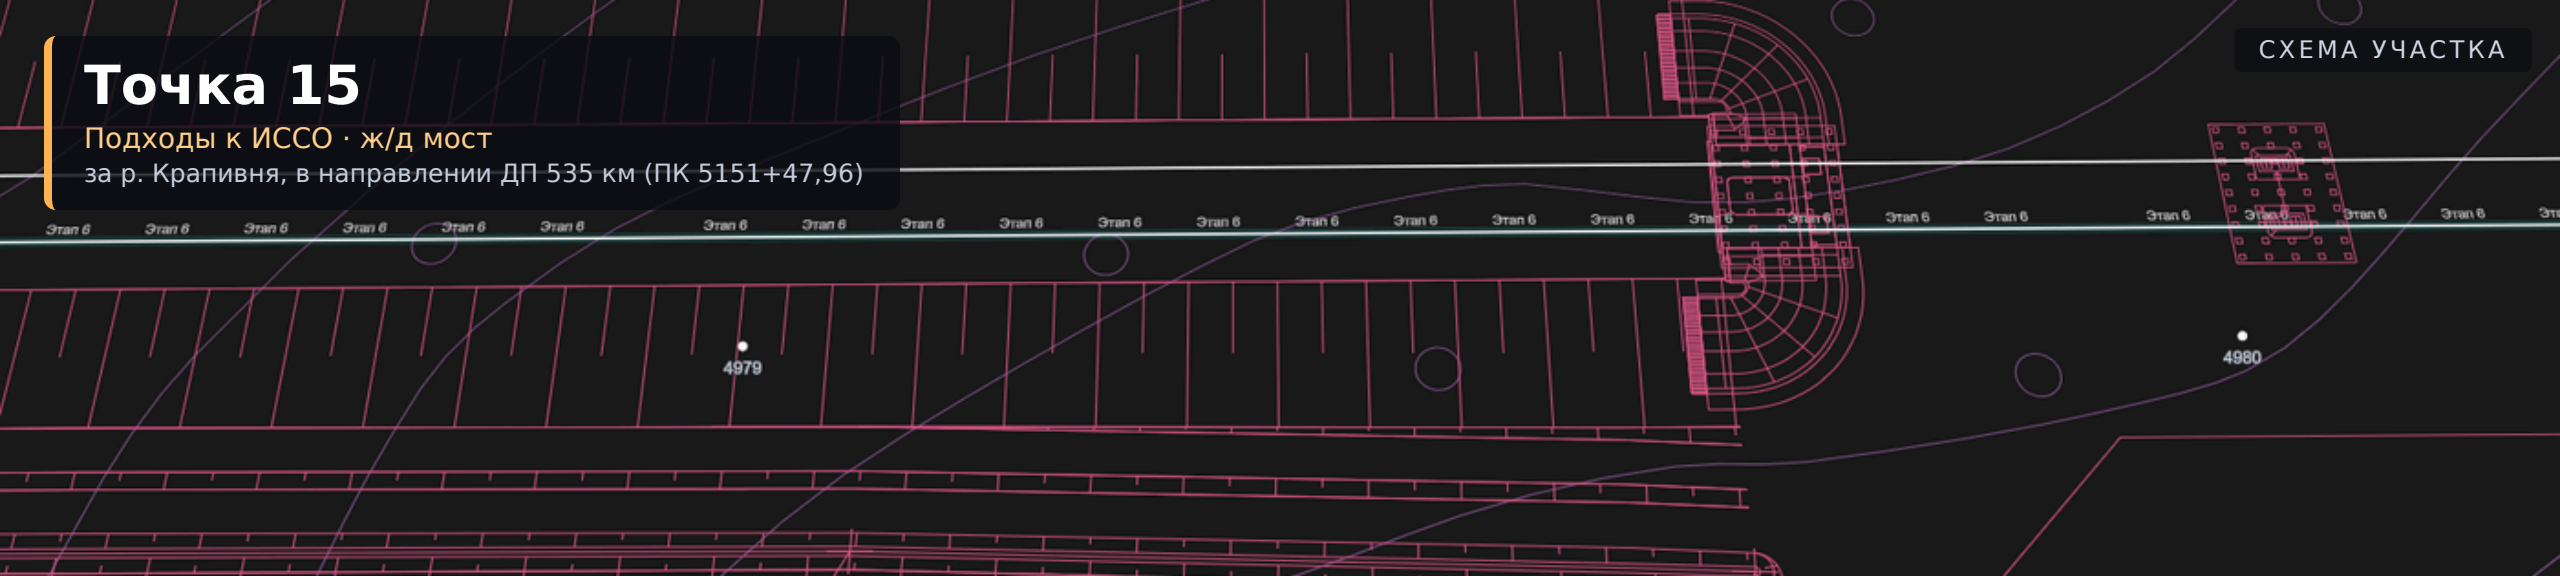


ФОТО С КВАДРОКОПТЕРА



ПК 4979+57,75 - ПК 4983+95,15

Подходы к мосту — насыпь VI типа. УПЖ 45,65 м, высота насыпи 8,13 м; УПЖ 44,05 м, высота насыпи 7,81 м.

Точка 16

Подходы к ИССО · ж/д эстакада

за р. Крапивня, в направлении ДП 535 км (ПК 5151+47,96)

ФОТО С КВАДРОКОПТЕРА

ПК 4995+01,26 - ПК 4994+11,66

Подход на ПК 4995+01,26 — насыпь VI типа, УПЖ 43,6 м, высота насыпи 7,72 м. Подход на ПК 4994+11,66 — насыпь IX типа, УПЖ 41,15 м, высота насыпи 7,23 м.

Отдельная схема расположения для точки 16 в исходных материалах отсутствует.

Точка 17

Подходы к ИССО · ж/д мост

за р. Крапивня, в направлении ДП 535 км (ПК 5151+47,96)

СХЕМА УЧАСТКА

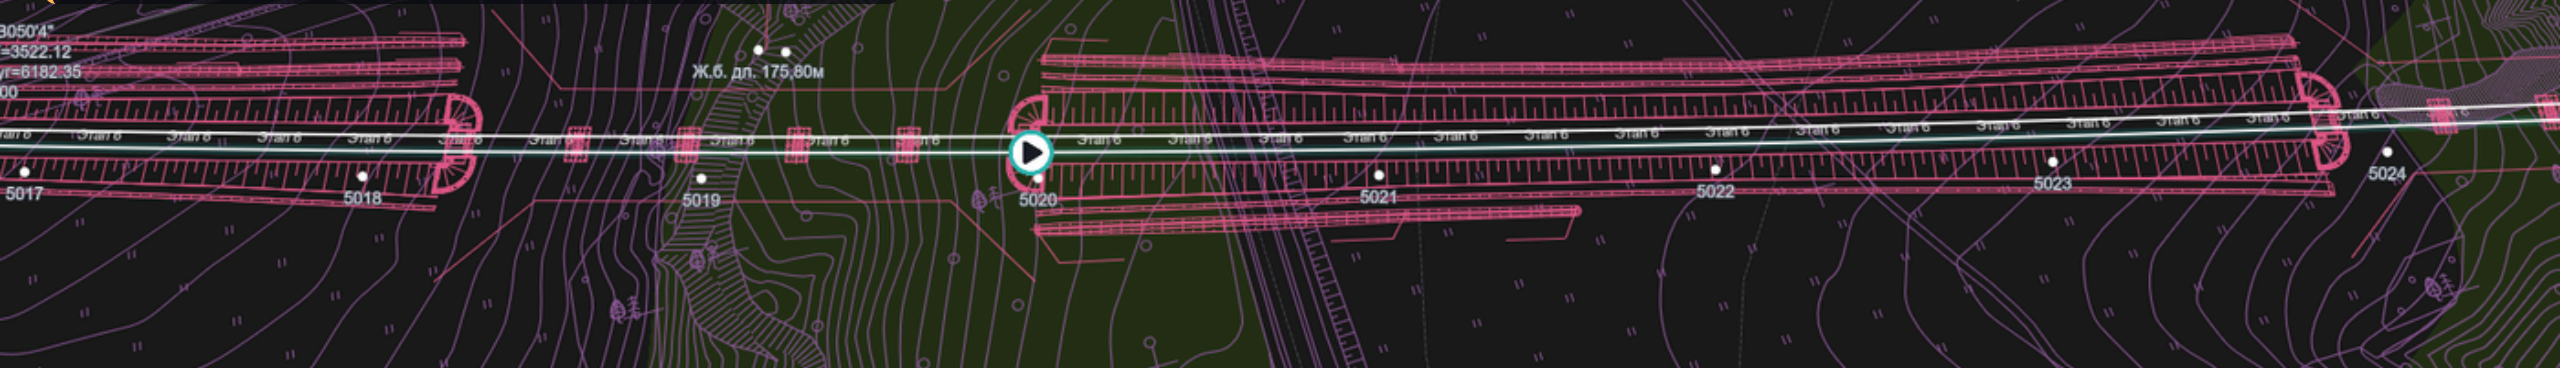


ФОТО С КВАДРОКОПТЕРА



ПК 5018+16,04 - ПК 5019+91,87

Подход на ПК 5018+16,04 — насыпь XII типа, УПЖ 38,05 м, высота насыпи 6,61 м. Подход на ПК 5019+91,87 — насыпь XIV типа, УПЖ 43,25 м, высота насыпи 7,65 м.

Точка 18

Подходы к ИССО · ж/д мост

за р. Крапивня, в направлении ДП 535 км (ПК 5151+47,96)

СХЕМА УЧАСТКА

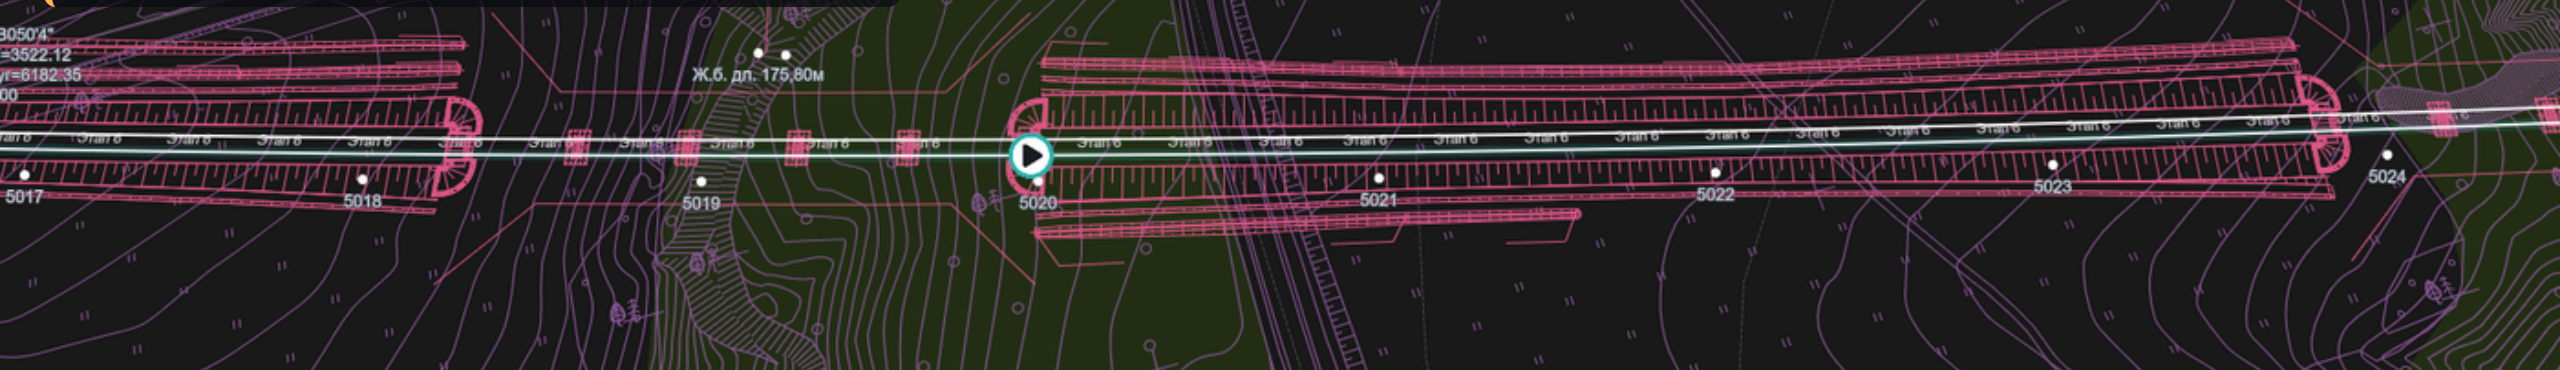


ФОТО С КВАДРОКОПТЕРА

ПК 5023+72,05 - ПК 5028+09,53

Подход на ПК 5023+72,05 — насыпь XIV типа, УПЖ 42,8 м, высота насыпи 7,56 м. Подход на ПК 5028+09,53 — насыпь VII типа, УПЖ 38,1 м, высота насыпи 6,62 м.

Точка 19

Подходы к ИССО · ж/д мост

за р. Крапивня, в направлении ДП 535 км (ПК 5151+47,96)

СХЕМА УЧАСТКА


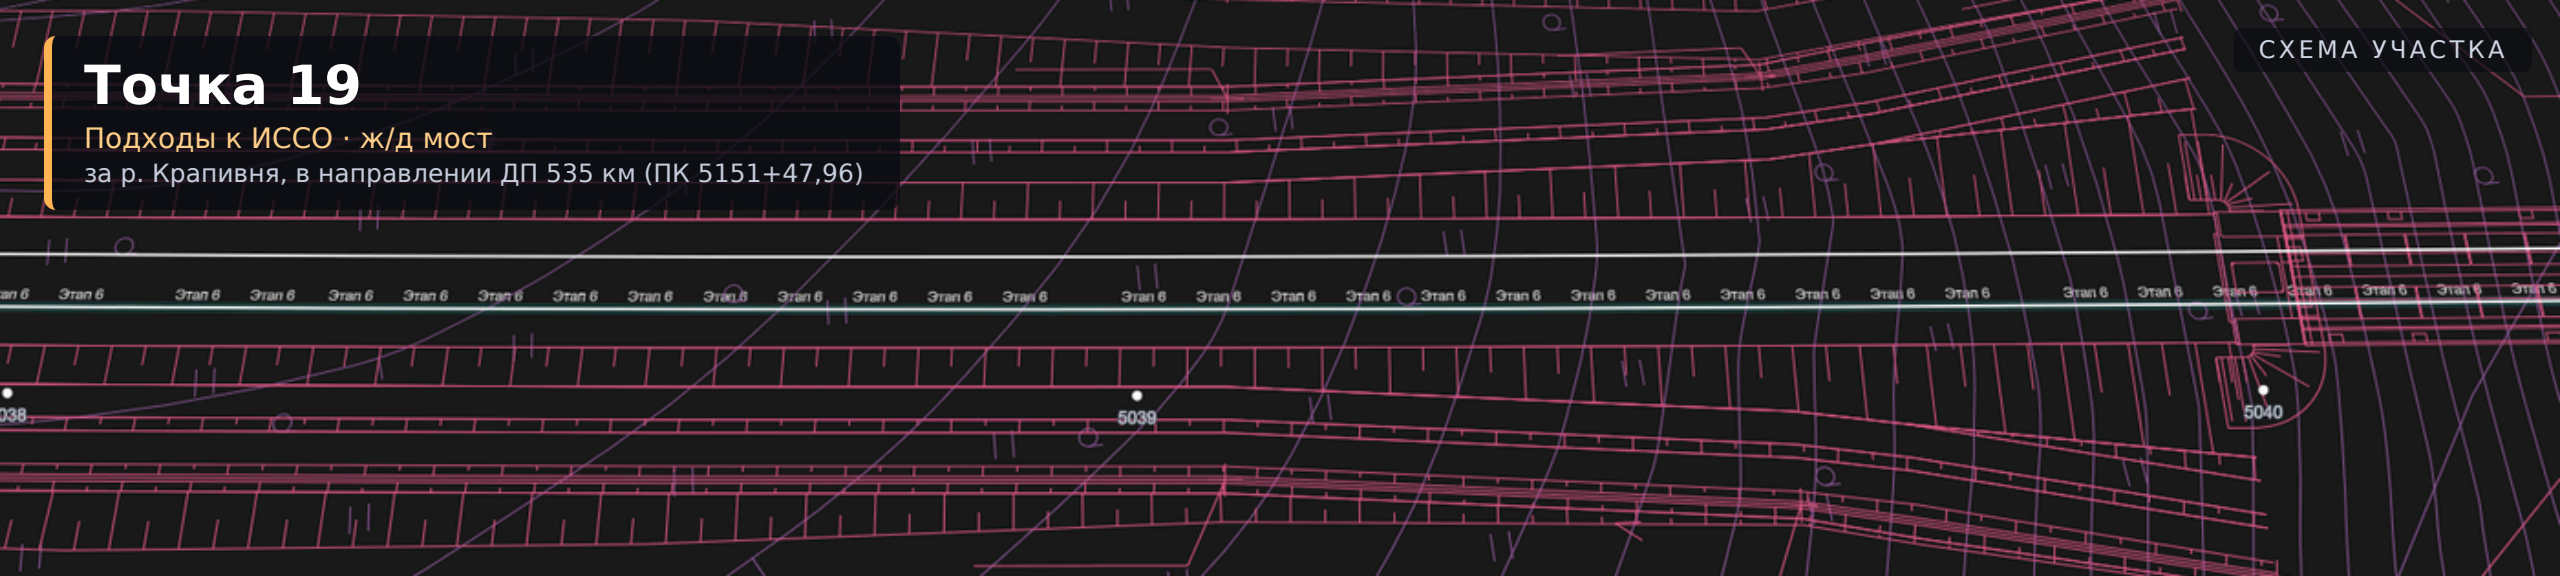


ФОТО С КВАДРОКОПТЕРА

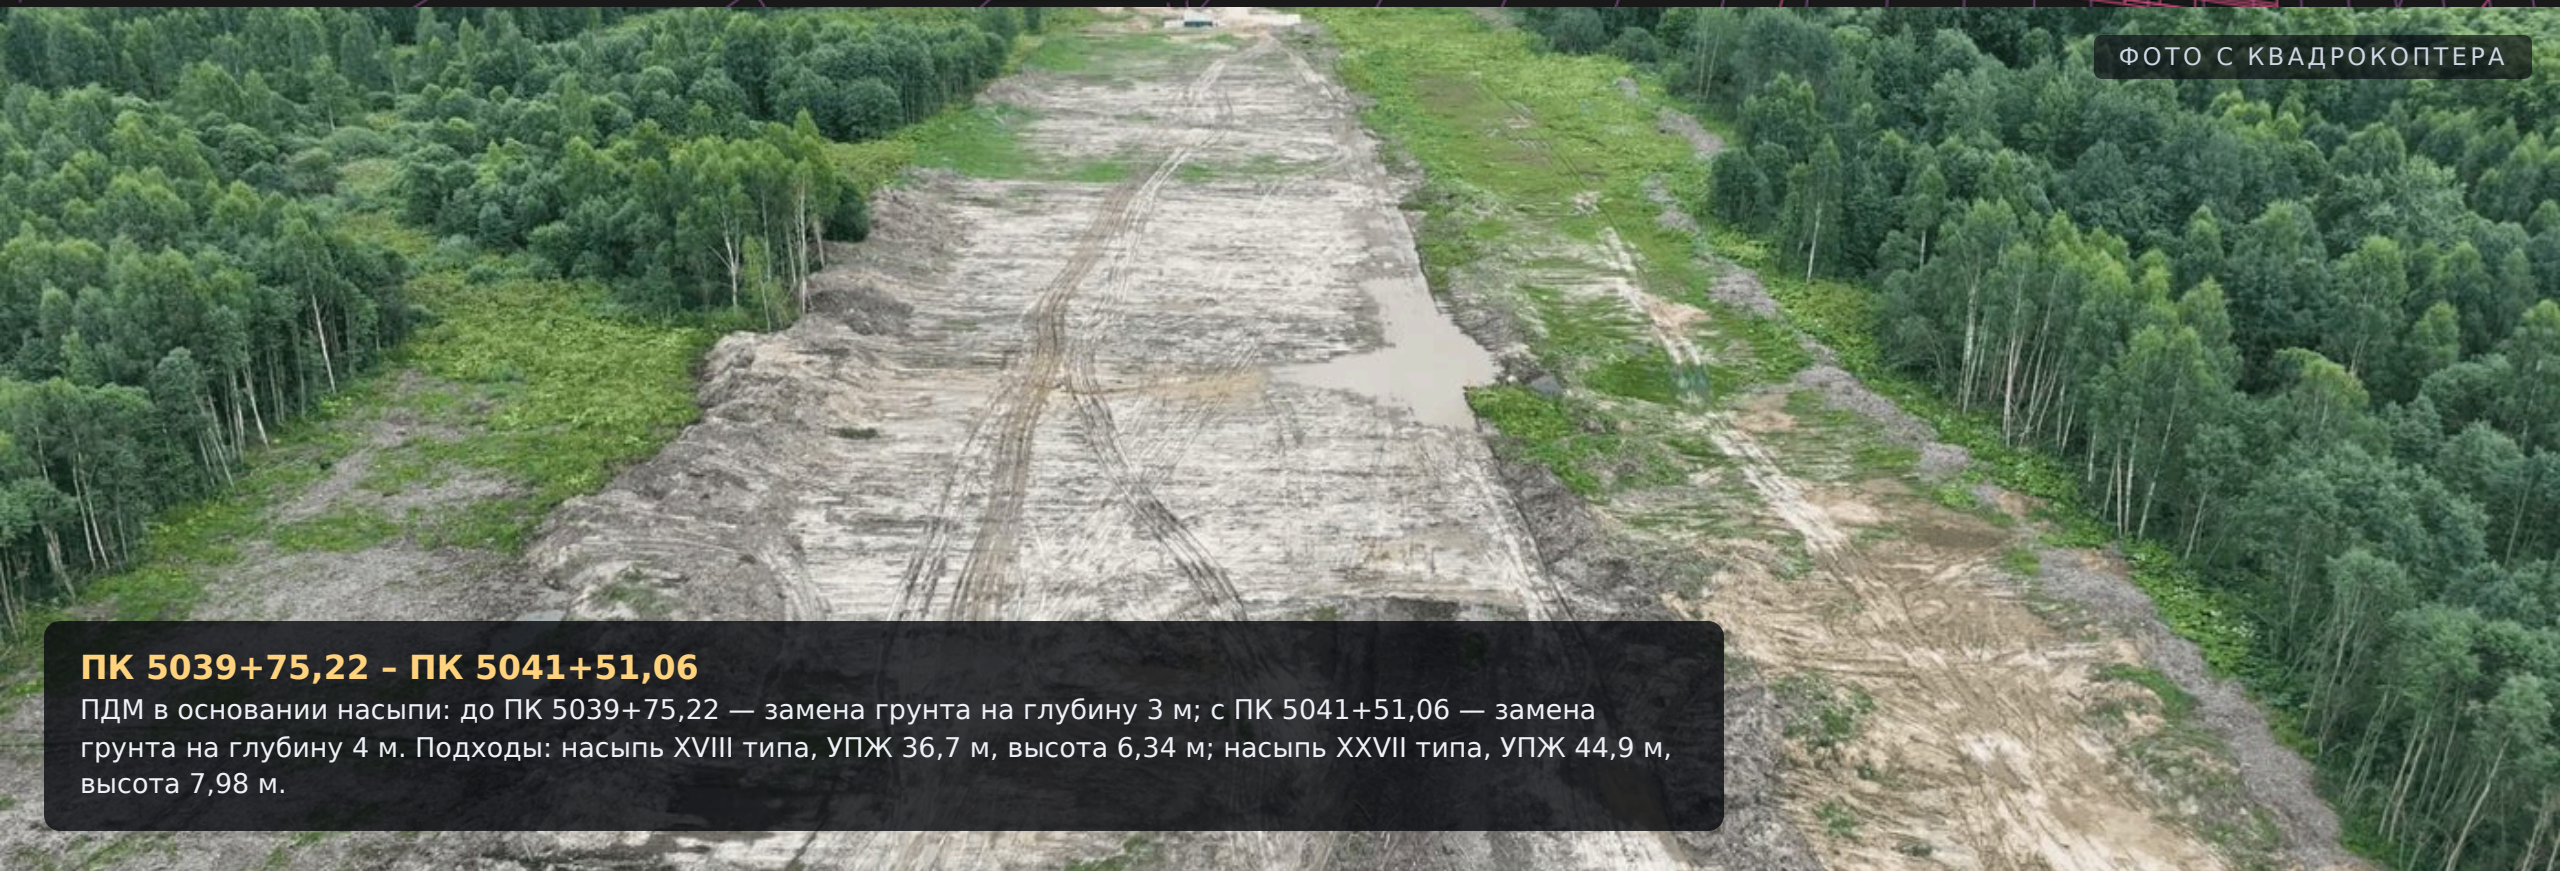

ПК 5039+75,22 - ПК 5041+51,06

ПДМ в основании насыпи: до ПК 5039+75,22 — замена грунта на глубину 3 м; с ПК 5041+51,06 — замена грунта на глубину 4 м. Подходы: насыпь XVIII типа, УПЖ 36,7 м, высота 6,34 м; насыпь XXVII типа, УПЖ 44,9 м, высота 7,98 м.

Точка 20

Подходы к ИССО · ж/д мост
за р. Крапивня, в направлении ДП 535 км (ПК 5151+47,96)

СХЕМА УЧАСТКА

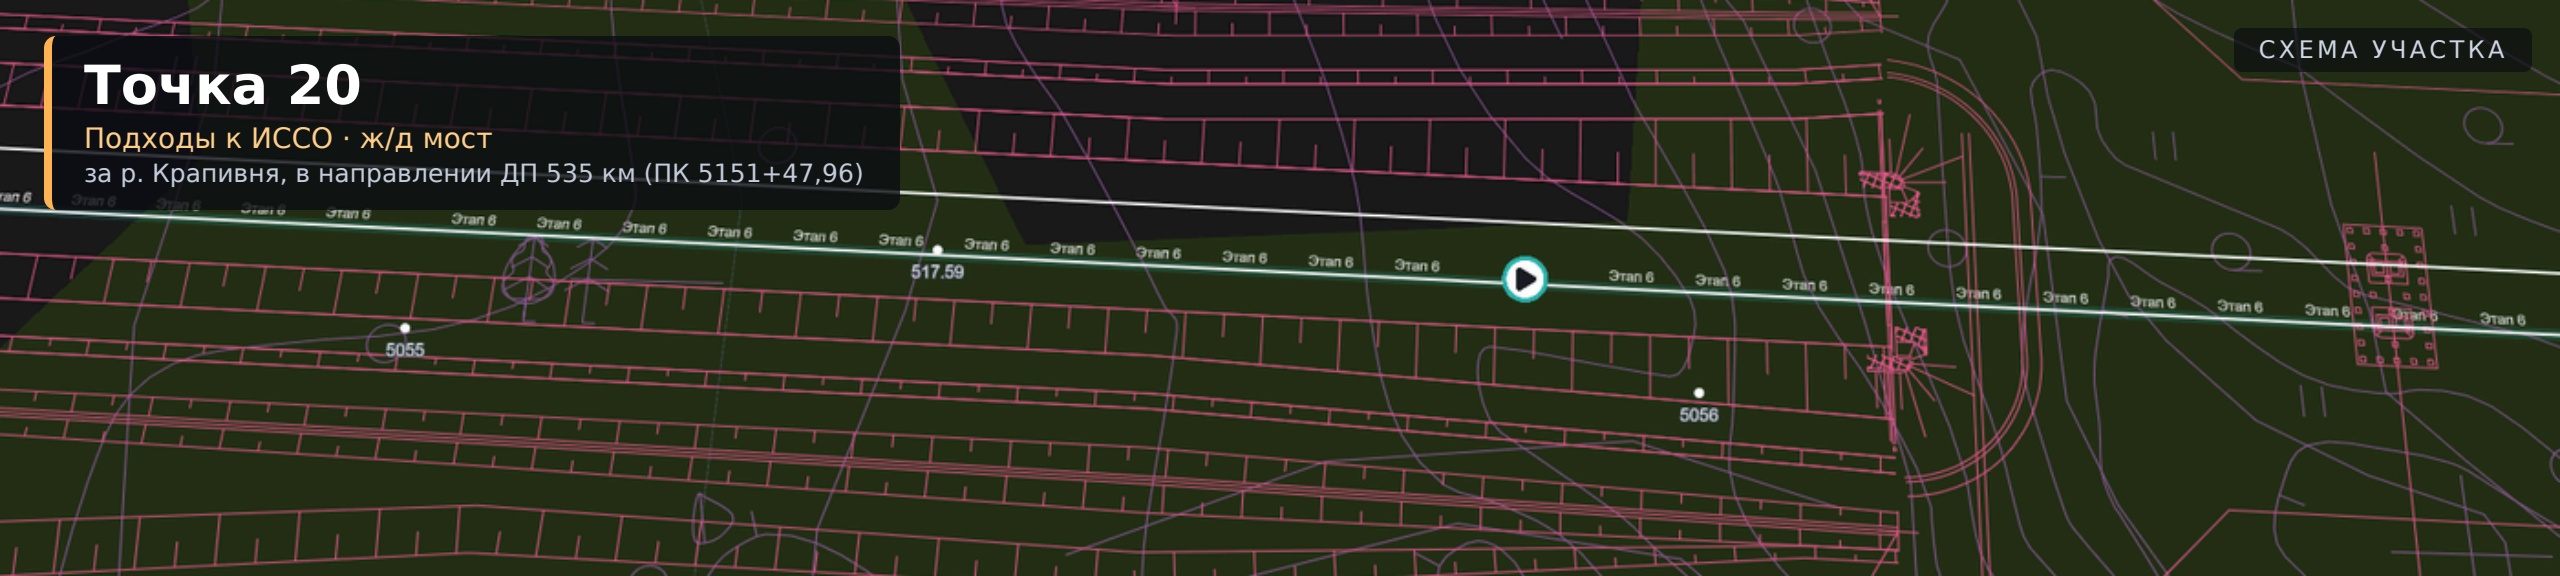


ФОТО С КВАДРОКОПТЕРА




ПК 5056+07,04 - ПК 5061+09,80

ПДМ в основании насыпи до ПК 5056+07,04 — замена грунта на глубину 1 м. Подходы: насыпь XXIII типа, УПЖ 29,4 м, высота 4,88 м; насыпь XXIII типа, УПЖ 26,1 м, высота 4,22 м.

Точка 21

Подходы к ИССО · ж/д путепровод
за ДП 535 км (ПК 5151+47,96), в направлении р. Шоша

СХЕМА УЧАСТКА

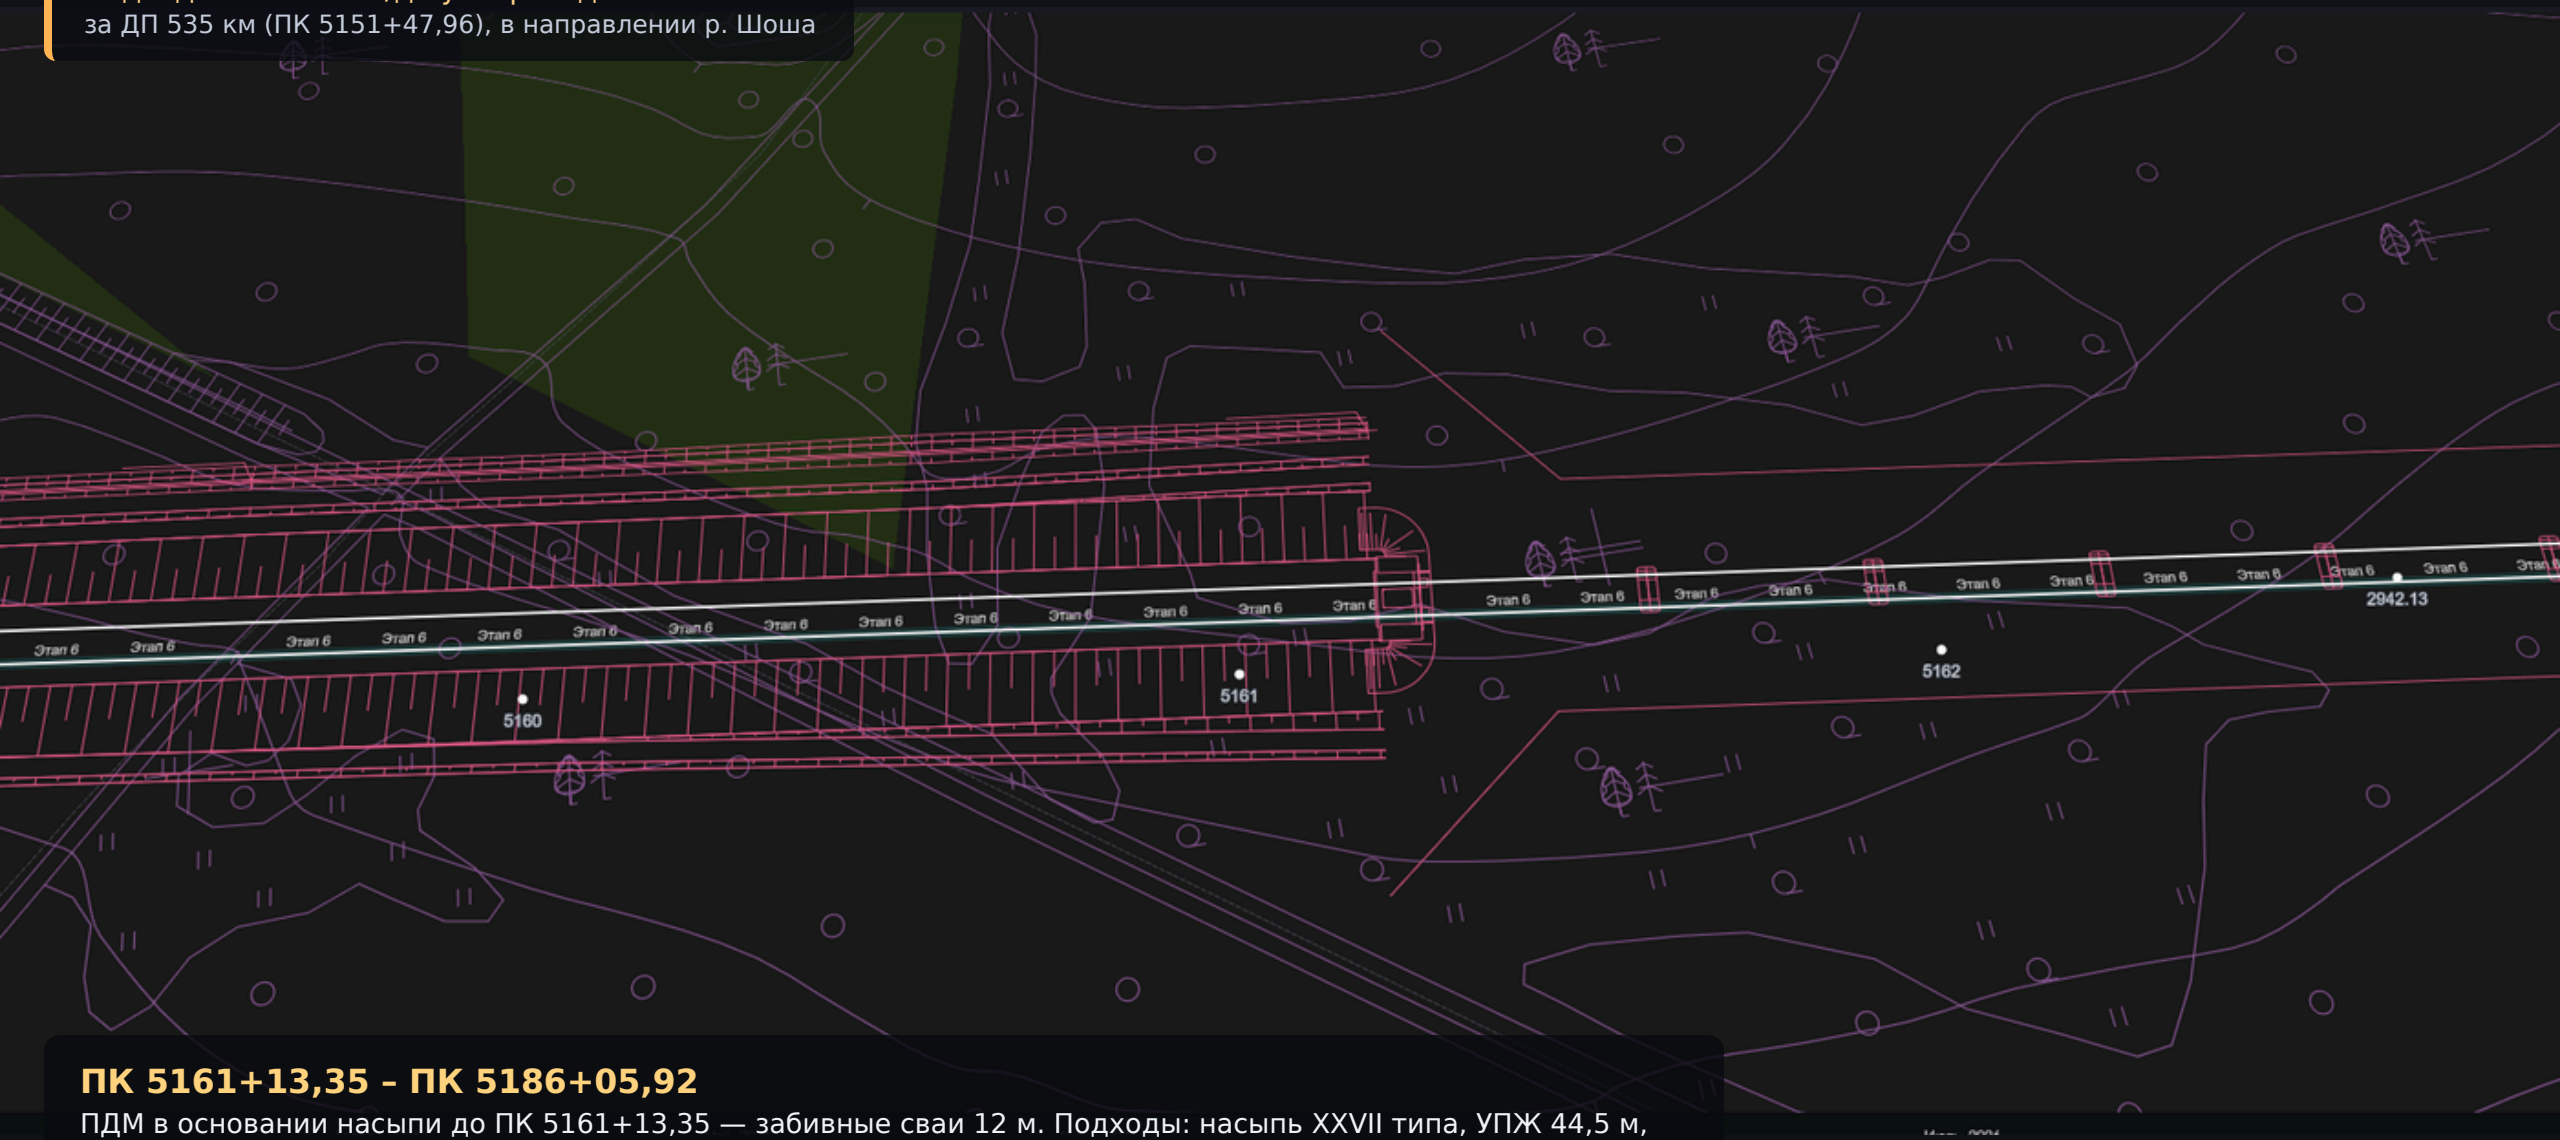

ПК 5161+13,35 - ПК 5186+05,92

ПДМ в основании насыпи до ПК 5161+13,35 — забивные сваи 12 м. Подходы: насыпь XXVII типа, УПЖ 44,5 м, высота 7,9 м; насыпь XXIX типа, УПЖ 44,3 м, высота 7,86 м.

Фото с квадрокоптера для точки 21 в исходных материалах отсутствует.

Точка 22

Подходы к ИССО · ж/д путепровод
за ДП 535 км (ПК 5151+47,96), в направлении р. Шоша

СХЕМА УЧАСТКА

ФОТО С КВАДРОКОПТЕРА

ПК 5202+40,30 - ПК 5206+99,10

ПДМ: до ПК 5202+40,30 — забивные сваи 17 м + замена грунта на глубину 4 м; с ПК 5206+99,10 — замена грунта на глубину 1 м. Подходы: насыпи XXXVII и XXIX типов, УПЖ не предусмотрено.

Точка 23

Подходы к ИССО · ж/д мост

за ДП 535 км (ПК 5151+47,96), в направлении р. Шоша

СХЕМА УЧАСТКА

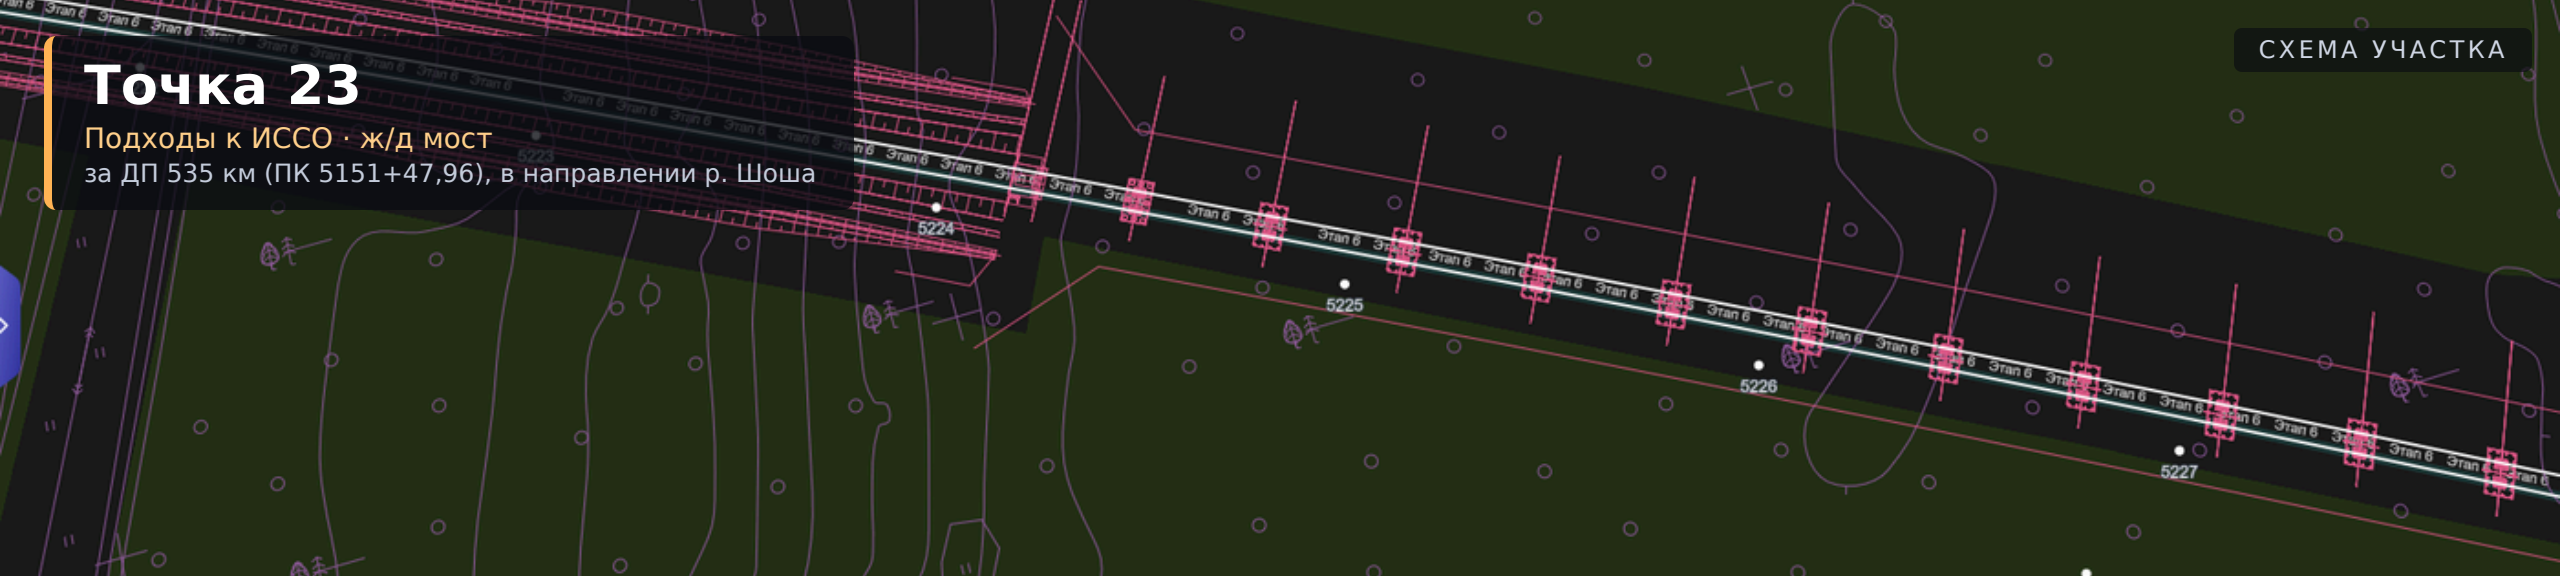


ФОТО С КВАДРОКОПТЕРА



ПК 5224+08,43 - ПК 5255+43,55

ПДМ: до ПК 5224+08,43 — забивные сваи 9 м + замена грунта 1 м; с ПК 5255+43,55 — забивные сваи 9 м + замена грунта 2 м. Подходы: насыпь XLII типа, УПЖ 25,15 м, высота 4,03 м; насыпь XLIII типа, УПЖ 48,1 м, высота 8,62 м.

Точка 24

Подходы к ИССО · ж/д мост (р. Шоша)
р. Шоша

СХЕМА УЧАСТКА

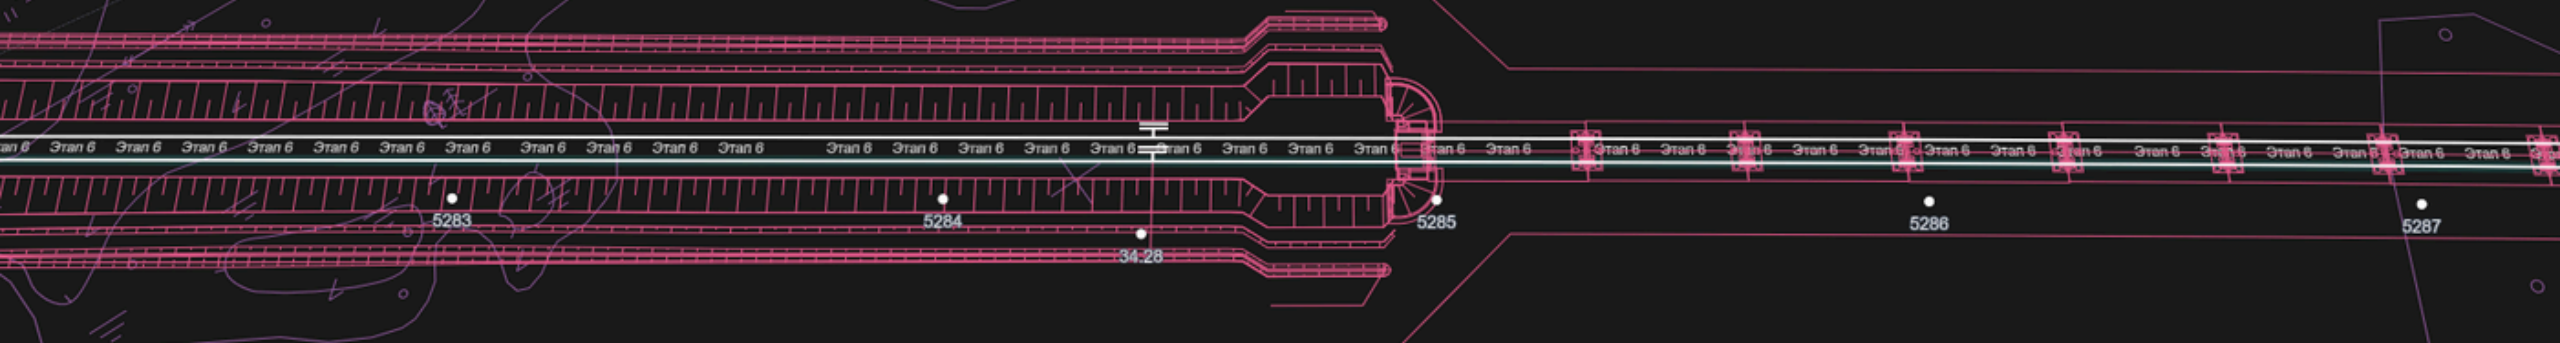


ФОТО С КВАДРОКОПТЕРА

ПК 5284+83,62 - ПК 5367+59,32

ПДМ: до ПК 5284+83,62 — забивные сваи 15 м + замена грунта 2 м; с ПК 5367+59,32 — замена грунта на глубину 1 м. Подходы: насыпь LV типа, УПЖ 30,95 м, высота 5,19 м; насыпь XXXVIII типа, УПЖ 43,25 м, высота 7,65 м.

Точка 25

Подходы к ИССО · ж/д мост
за р. Шоша, в направлении Высоково

СХЕМА УЧАСТКА

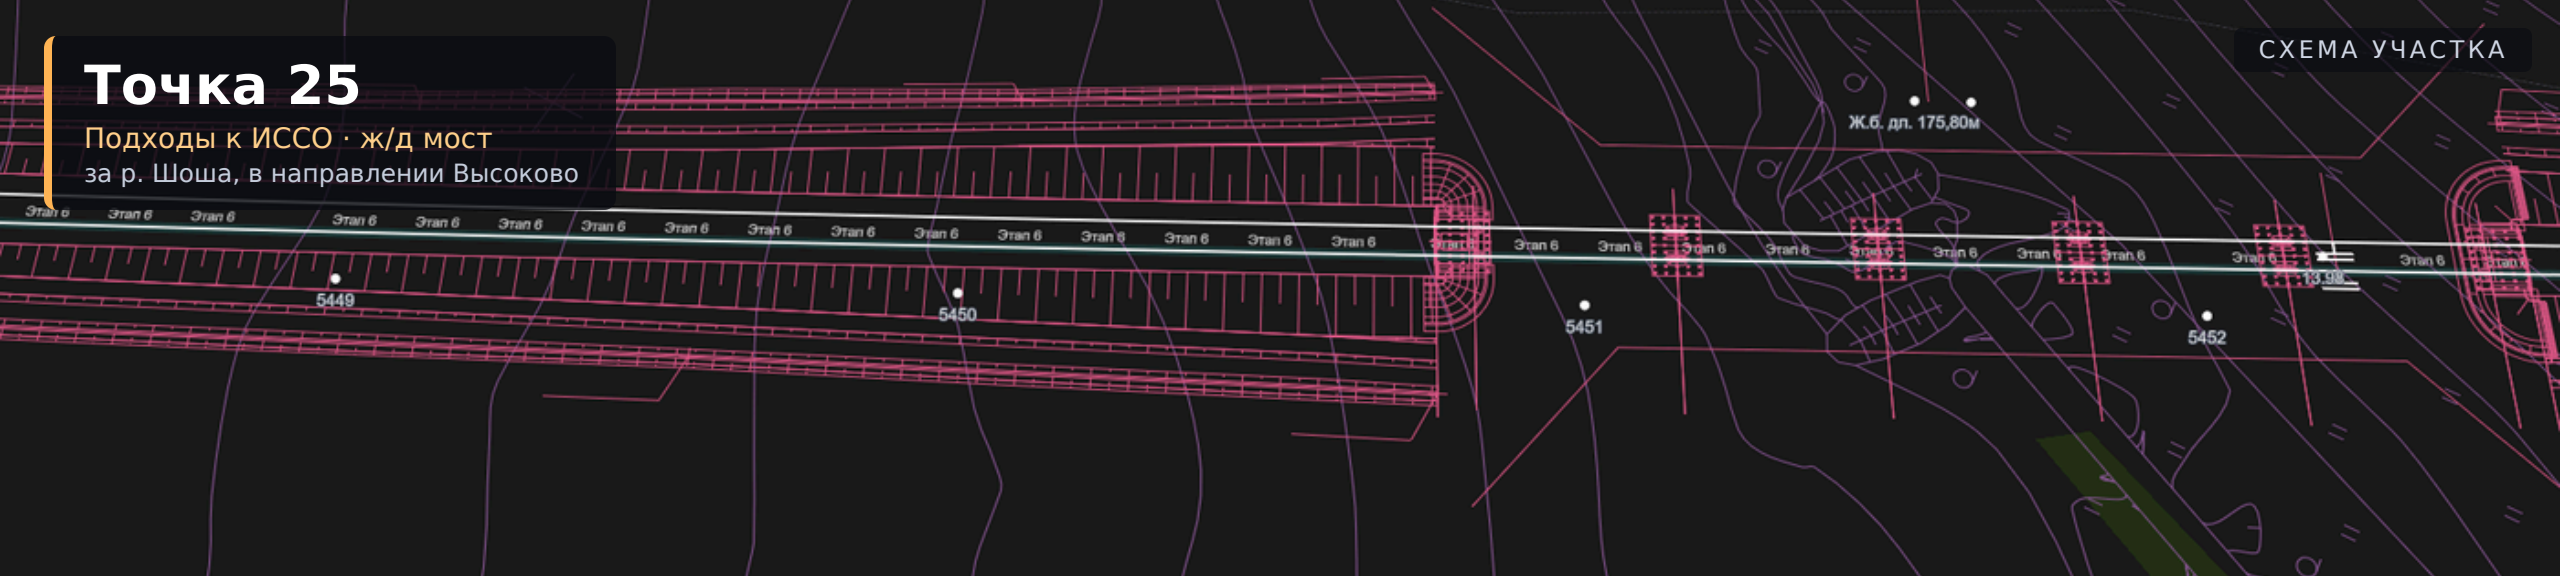


ФОТО С КВАДРОКОПТЕРА



ПК 5450+68,73 - ПК 5452+44,53

ПДМ: до ПК 5450+68,73 — замена грунта на глубину 4 м; с ПК 5452+44,53 — замена грунта на глубину 3 м.
Подходы: насыпь XXXVIII типа, УПЖ 42,25 м, высота 7,45 м; насыпь XXXVIII типа, УПЖ 39,5 м, высота 6,9 м.

Точка 26

Подходы к ИССО · ж/д мост
за р. Шоша, в направлении Высоково

СХЕМА УЧАСТКА



ФОТО С КВАДРОКОПТЕРА



ПК 5481+13,72 - ПК 5482+89,49

ПДМ: до ПК 5481+13,72 — забивные сваи 14 м; с ПК 5482+89,49 — забивные сваи 14 м + замена грунта 3 м.

Подходы: насыпь XXXVIII типа, УПЖ 46,6 м, высота 8,32 м; насыпь XXXIX типа, УПЖ 36,05 м, высота 6,21 м.

Точка 27

Подходы к ИССО · ж/д мост
за р. Шоша, в направлении Высоково

СХЕМА УЧАСТКА



ФОТО С КВАДРОКОПТЕРА



ПК 5504+05,60 - ПК 5523+64,13


ПДМ: до ПК 5504+05,60 — забивные сваи 14 м + замена грунта 4 м; с ПК 5523+64,13 — забивные сваи 21 м.

Подходы: насыпь LXXIV типа, УПЖ 43,7 м, высота 7,74 м; насыпь LXXV типа, УПЖ 44,15 м, высота 7,83 м.

Точка 28

Подходы к ИССО · ж/д мост
ст. Высоково, в направлении р. Шоша

СХЕМА УЧАСТКА

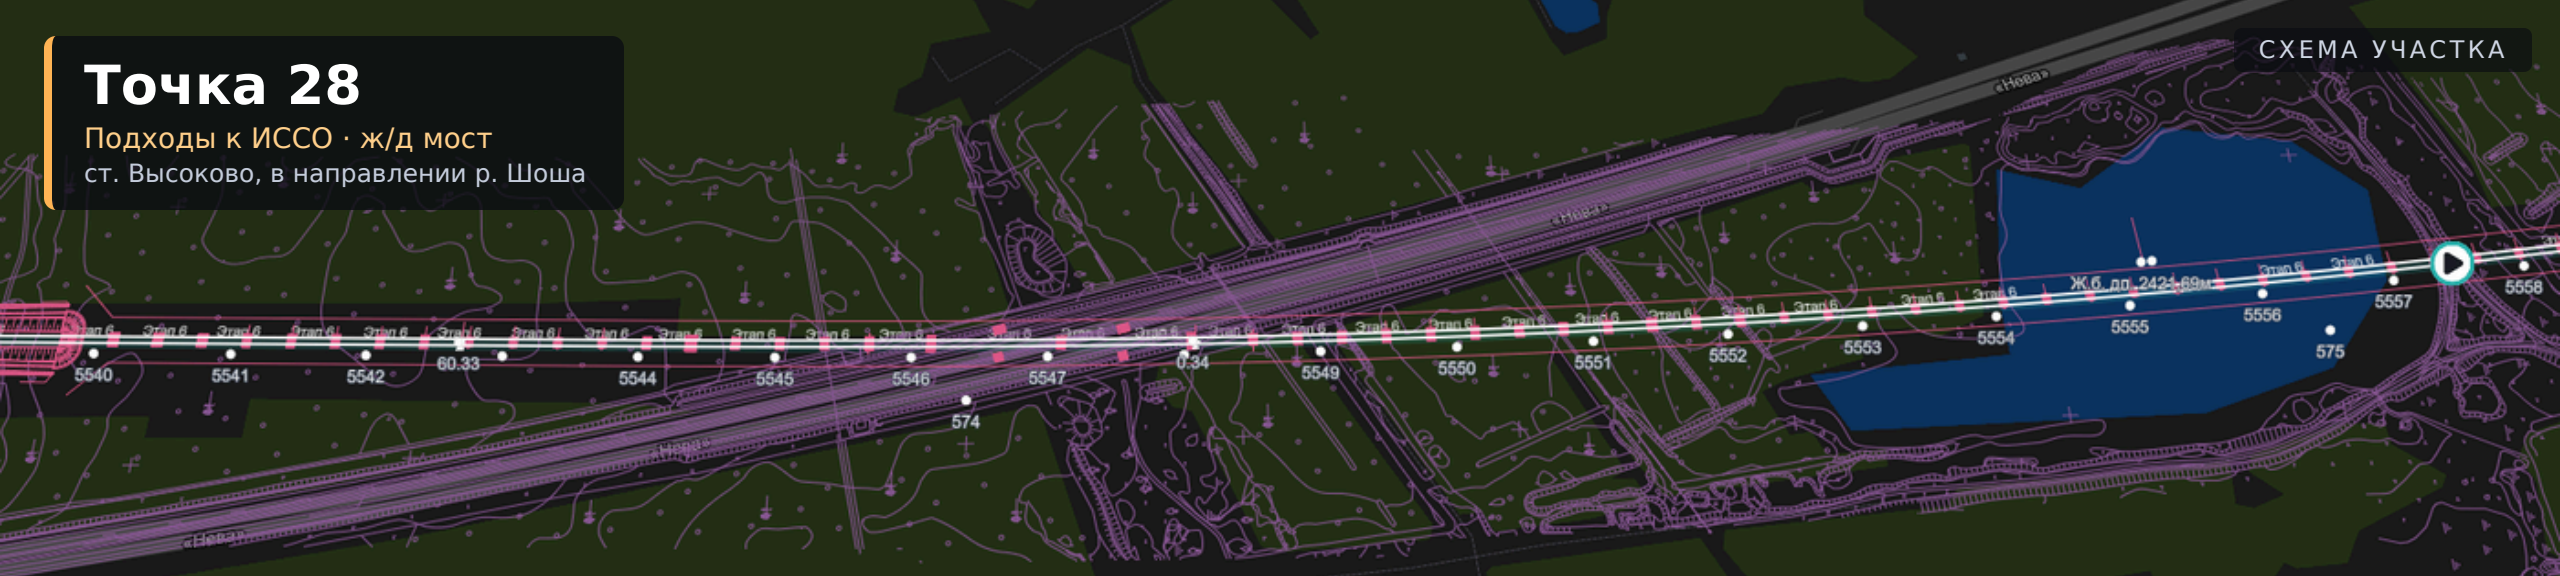

Начало участка



Конец участка



ФОТО С КВАДРОКОПТЕРА


ПК 5543+04,52 - ПК 5558+50,65

ПДМ: до ПК 5543+04,52 — забивные сваи 13 м + замена грунта 4 м; с ПК 5558+50,65 — забивные сваи 10 м + замена грунта 4 м. Подходы: насыпь LXXIX типа, УПЖ 52,55 м, высота 9,51 м; насыпь LXXX типа, УПЖ 42 м, высота 7,4 м.


Точка 29

Подходы к ИССО · ж/д мост
ст. Высоково, в направлении р. Шоша

СХЕМА УЧАСТКА

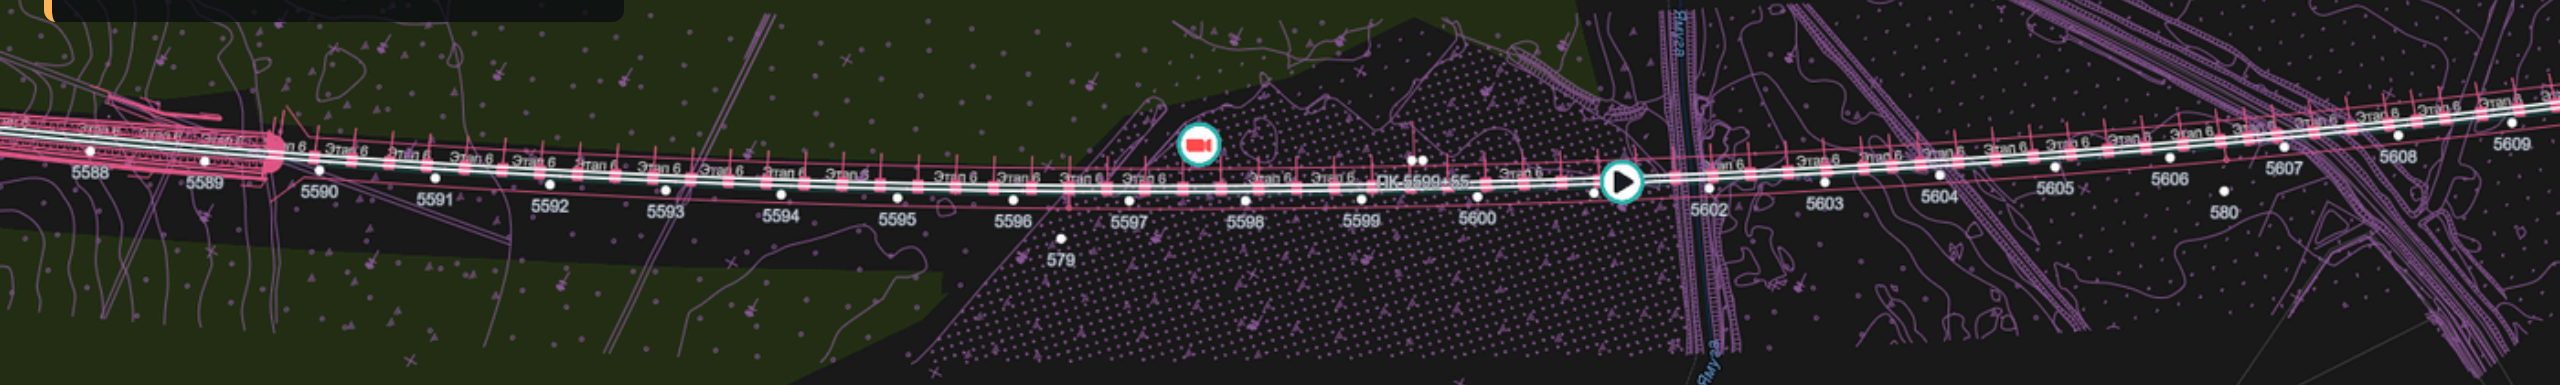

Начало участка

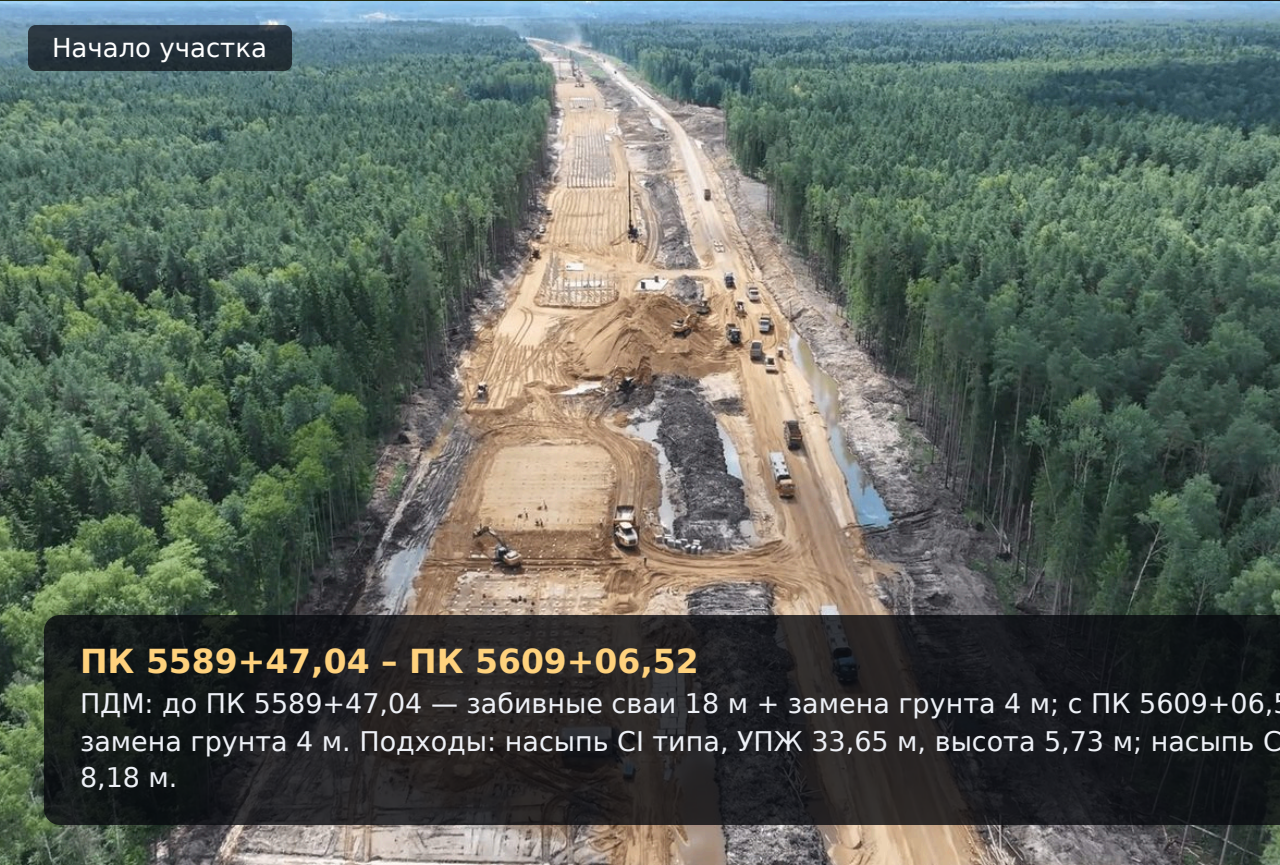

Конец участка



ФОТО С КВАДРОКОПТЕРА

ПК 5589+47,04 - ПК 5609+06,52

ПДМ: до ПК 5589+47,04 — забивные сваи 18 м + замена грунта 4 м; с ПК 5609+06,52 — забивные сваи 17 м + замена грунта 4 м. Подходы: насыпь CI типа, УПЖ 33,65 м, высота 5,73 м; насыпь CII типа, УПЖ 45,9 м, высота 8,18 м.

Точка 30

Высокие насыпи

ст. Высоково, в направлении р. Шоша

СХЕМА УЧАСТКА

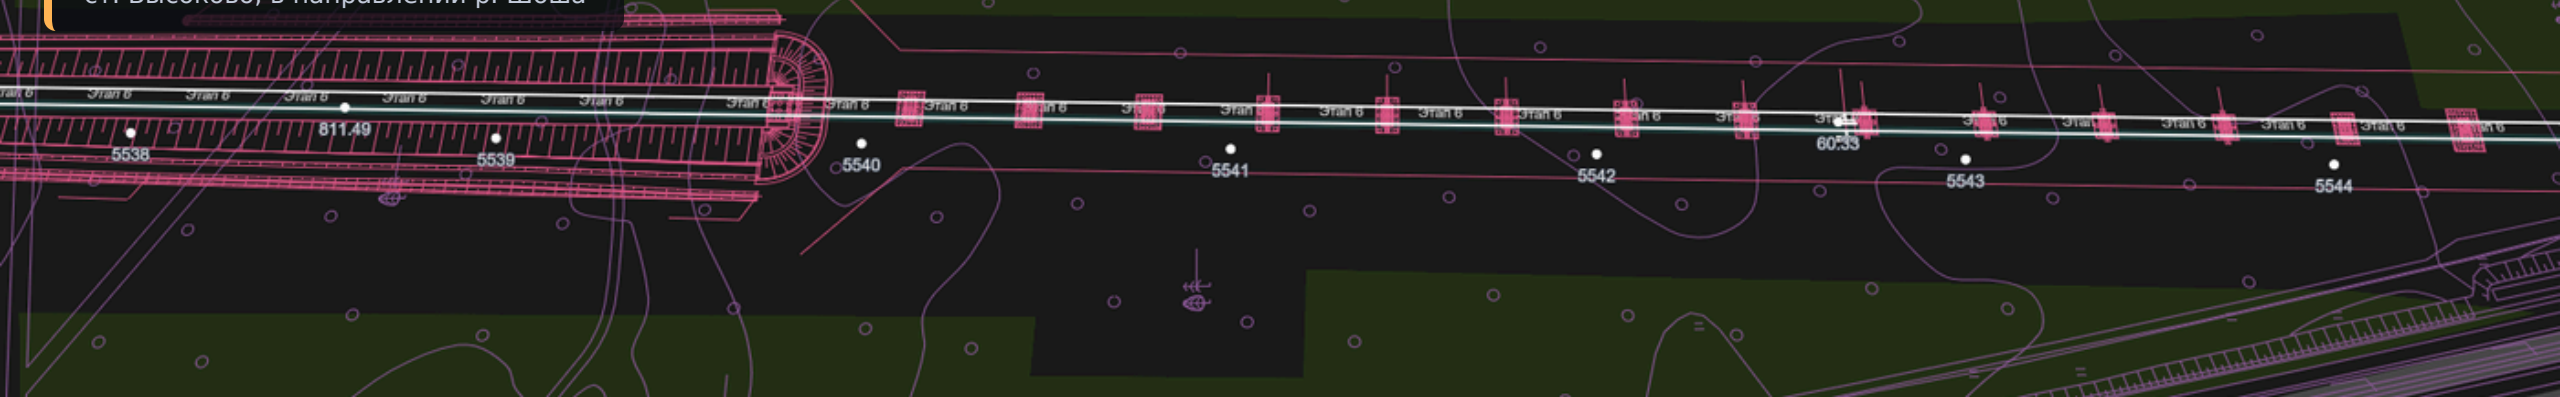


ФОТО С КВАДРОКОПТЕРА



ПК 5539+10,00 - ПК 5543+04,52 (участок установки: ПК 5542+40,00 - ПК 5542+60,00)

Насыпь максимальной высотой 10,15 м, LXXIX типа. ПДМ: забивные сваи 13 м + замена грунта на глубину 4 м. Опасные процессы: постоянное подтопление; карст — провалообразование исключается (категория неопасная).

Точка 31

Глубокие выемки

за р. Крапивня, в направлении ДП 535 км (ПК 5151+47,96)

СХЕМА УЧАСТКА


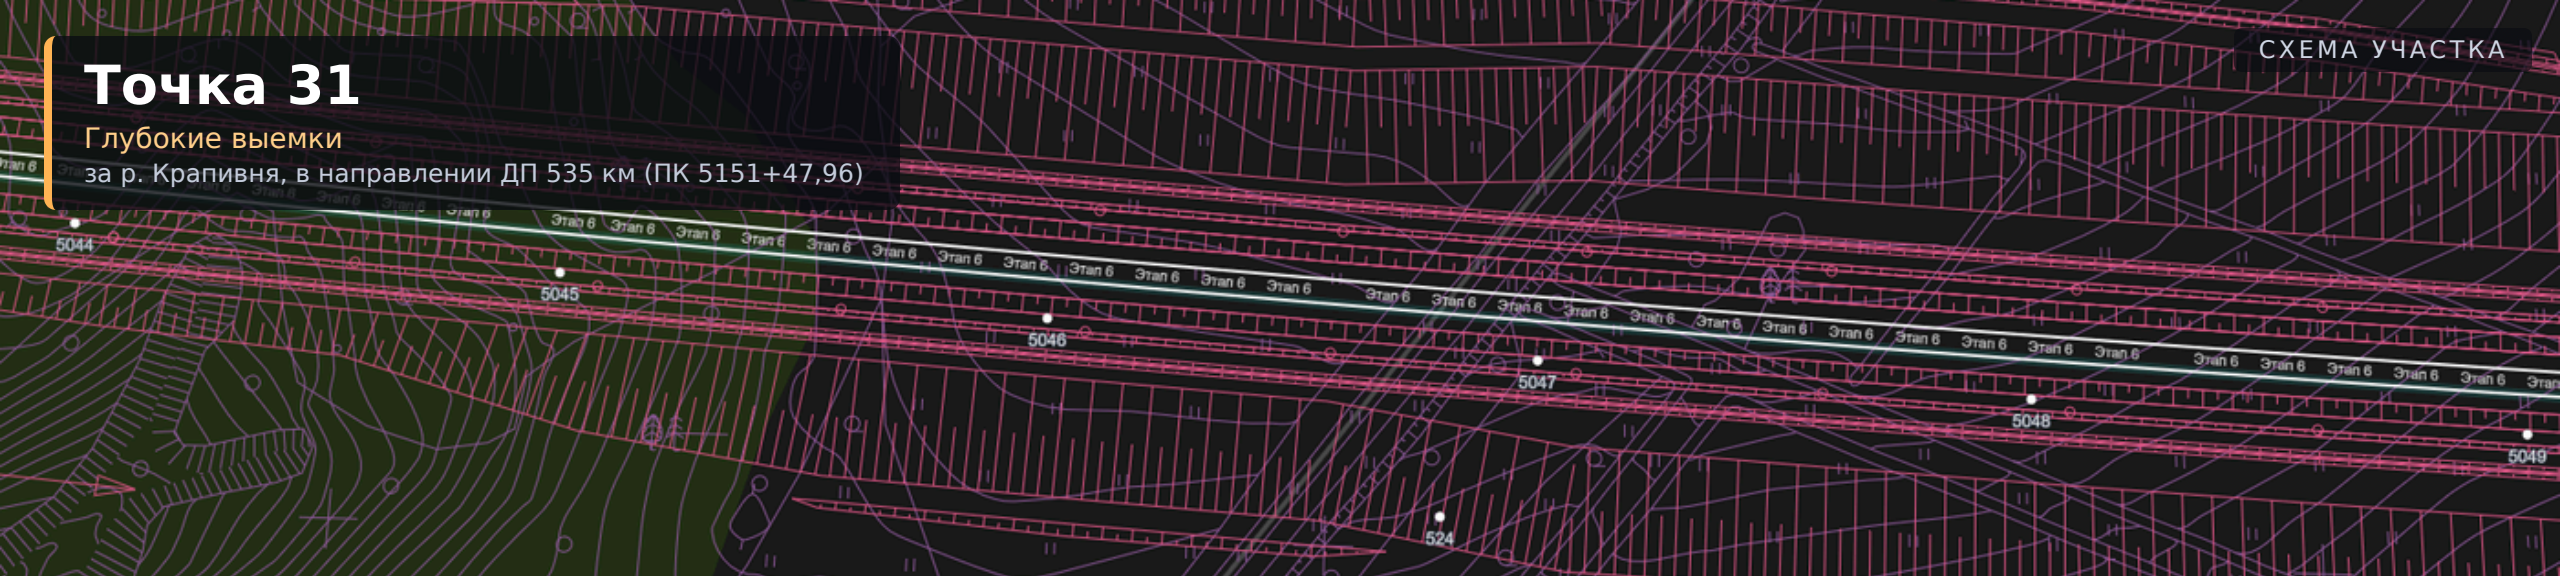


ФОТО С КВАДРОКОПТЕРА

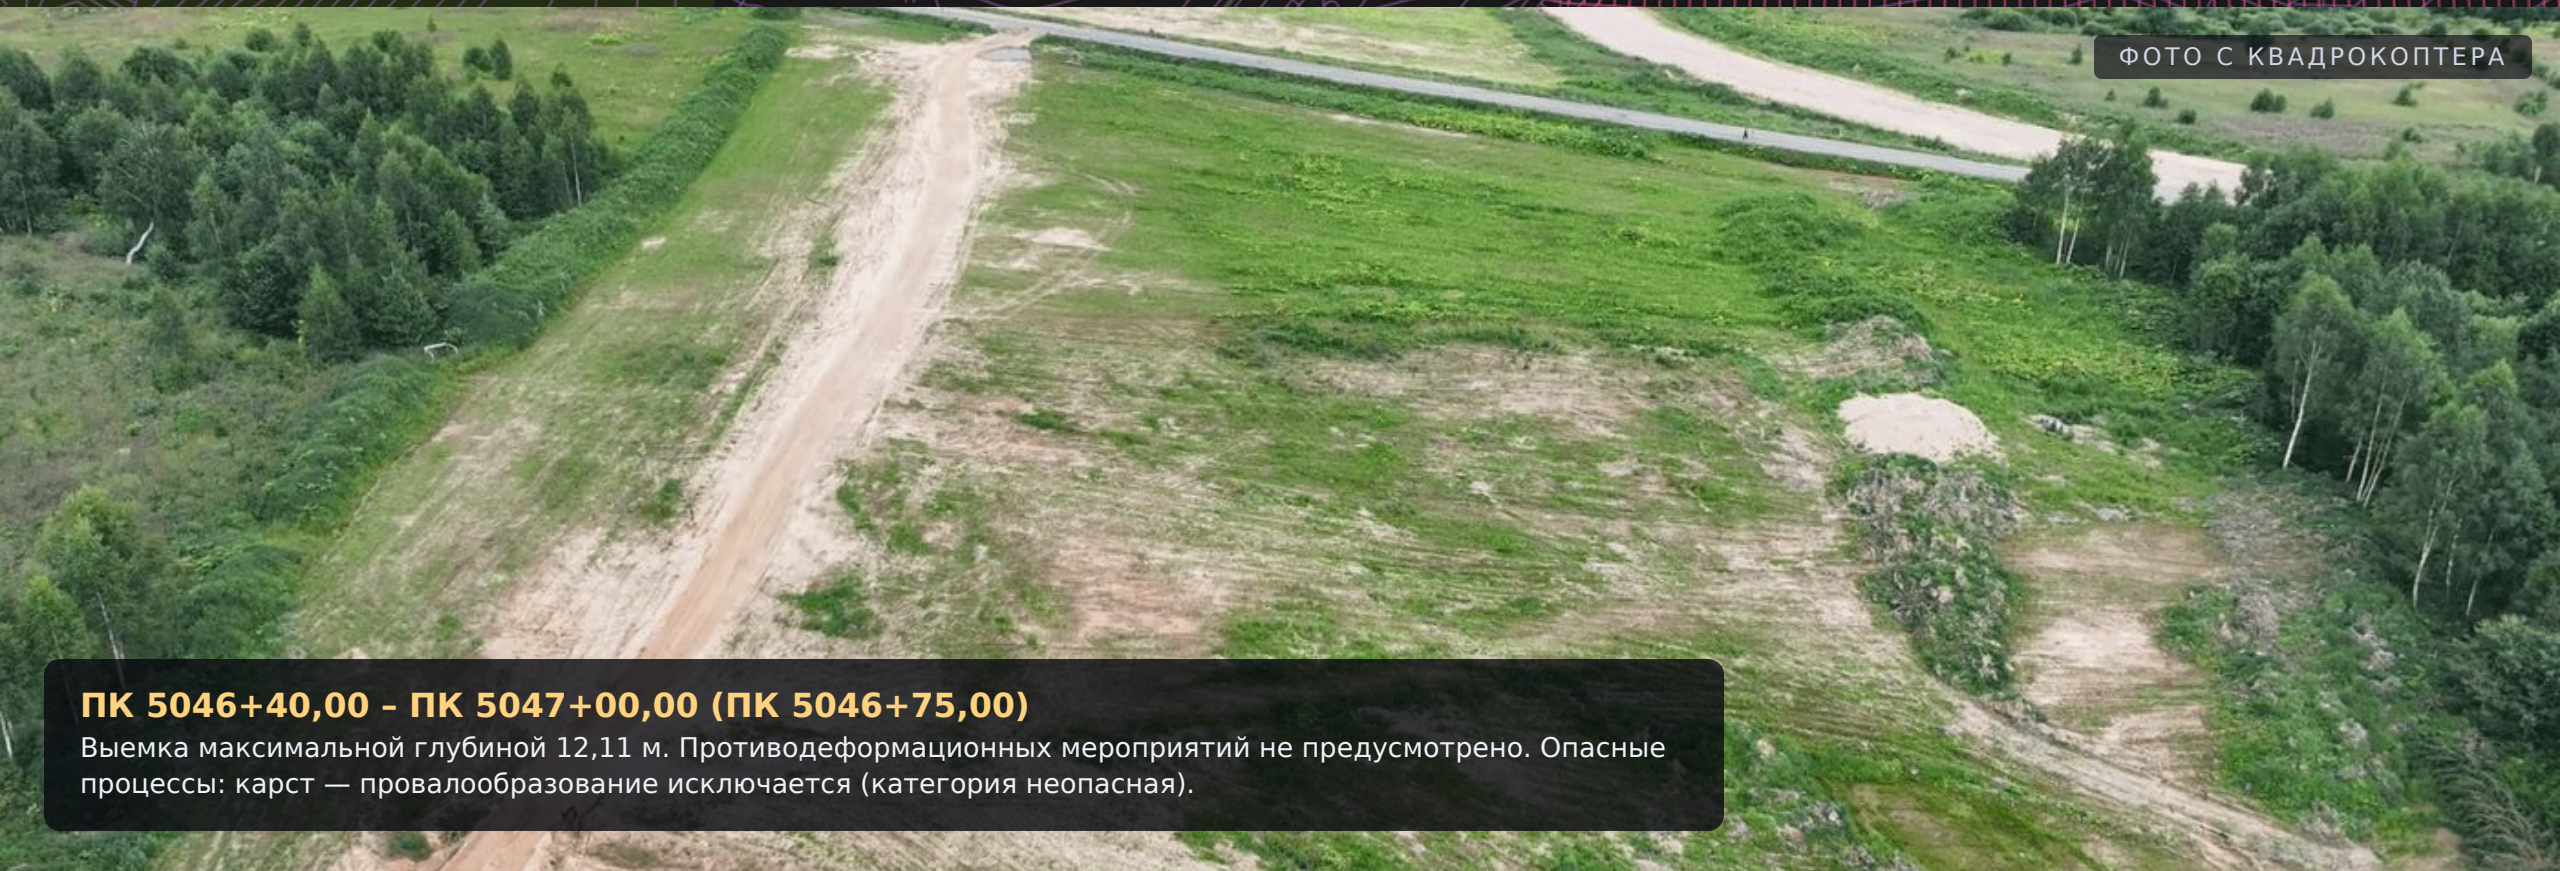

ПК 5046+40,00 - ПК 5047+00,00 (ПК 5046+75,00)

Выемка максимальной глубиной 12,11 м. Противодеформационных мероприятий не предусмотрено. Опасные процессы: карст — провалообразование исключается (категория неопасная).